


The background of the entire page is a light gray topographic map pattern with thin, dark gray contour lines. A solid, vertical red stripe runs down the right side of the page, starting from the top and extending to the bottom.

# ARCHITECTURAL PORTFOLIO

*By Karolina Arriola*  
2024

# CONTENTS

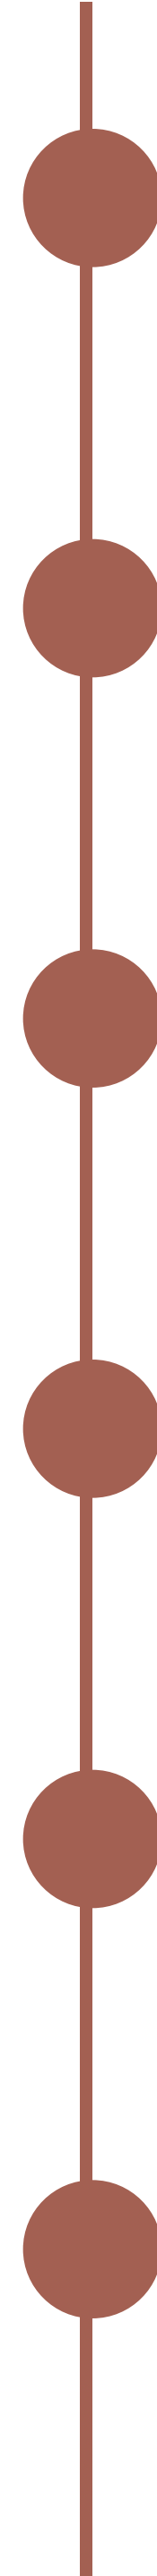

|                                       |
|---------------------------------------|
| Profile and Skills                    |
| Project 01 (NEO TRÓPICO)              |
| Project 02 (ENTRELACE LÚDICO)         |
| Project 03 (MUSEO DEL TRÓPICO)        |
| Project 04 (RESIDENCIAS DEL JARDÍN)   |
| Project 05 (RENDERS APARTAMENTOS SGM) |



# PROFILE

My name is Karolina Arriola, and I am delighted to introduce myself.

I'm a final year student at the Tecnológico de Costa Rica, where I'm completing my career in the exciting discipline of Architecture and Urbanism. My academic journey has been a constant place of discovery, curiosity and deep passion for architecture and design.

Throughout my career, I have cultivated a creative and proactive mindset and an ability to approach projects with focus dedication and a sense of leadership. My commitment to excellence is reflected in my constant search for innovative solutions and my desire to contribute significantly to the world of architecture.

Outside of architecture, one of my greatest interests has been photography, where I love to fuse architecture with the power of photography.

# SKILLS

## EDUCATION

**2014 - 2019** CTP de Ulloa. Técnico en Dibujo Arquitectónico

**2020 - today** TEC. Estudiante de Arquitectura y Urbanismo

## WORK EXPERIENCE

**2019 - 3 months** Internship as architectural draftman en Zürcher Architekten.

**2023 - today** Research Assistance. Digital Twin Teatro Nacional de Costa Rica, with professor Jose Pablo Bulgarelli.

**2024 - today** FL Arquitectura. Architectural designer.

## SOFTWARE SKILLS

|           |            |
|-----------|------------|
| REVIT     | ●●●●●●●●●● |
| AUTOCAD   | ●●●●●●●●●● |
| SKETCH UP | ●●●●●●●●●● |

PHOTOSHOP ●●●●●●●●●●

FIGMA ●●●●●●●●●●

ILLUSTRATOR ●●●●●●●●●●

ENSCAPE ●●●●●●●●●●

WORD ●●●●●●●●●●

POWERPOINT ●●●●●●●●●●

EXCEL ●●●●●●●●●●

| Software | Good | Not Good |
|----------|------|----------|
| MyMaps   | 8    | 4        |
| Mapbox   | 8    | 4        |
| FORMA    | 8    | 4        |
| QGIS     | 8    | 4        |

## SOFT SKILLS

|            |                     |
|------------|---------------------|
| Team work  | Work under pressure |
| Productive | Decision making     |
| Creative   | Problem resolution  |
| Leadership | Initiative          |
| Organized  |                     |

## LANGUAGES

Spanish: Native  
English: Intermediate  
French: Basic



# 01

## Neo Trópico

Propuesta de diseño para una torre de uso mixto en San Pablo de Heredia  
Taller 7




**Neo Trópico is a mixed-use project**, where you can live peacefully as there is commerce nearby. This tower seeks to be a space of comfort for all residents.

Neo Trópico has 6 floors, the first being for commercial use, the second for private amenities, and the third to sixth are apartments. The number of rooms per apartment was chosen according to the average age of users in the San Pablo de Heredia area.



In addition to designing the tower, the other requirement of this workshop was to create a masterplan of the entire lot, which was approximately 25 thousand m2.



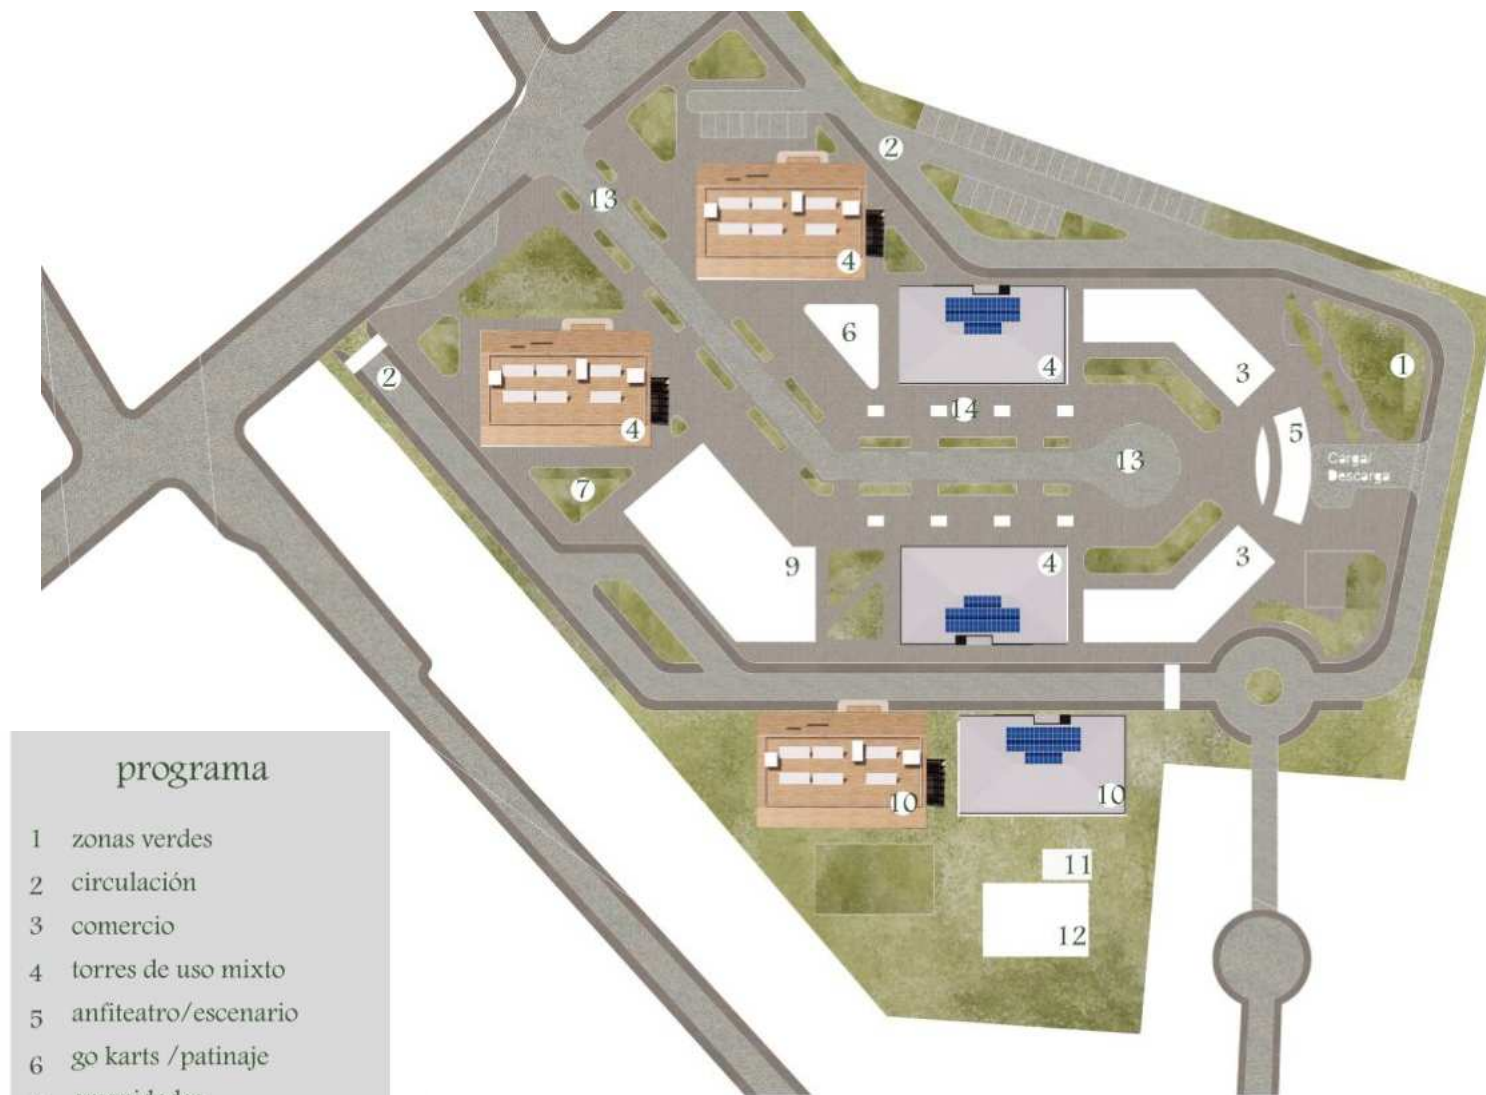


### programa


- 1 zonas verdes
- 2 circulación
- 3 comercio
- 4 torres de uso mixto
- 5 anfiteatro/escenario
- 6 go karts /patinaje
- 7 amenidades
- 8 parqueos externos
- 9 hotel
- 10 torres residenciales
- 11 planta de tratamientos
- 12 planta de retención pluvial
- 13 acceso vehículos de emergencia
- 14 quioscos comerciales

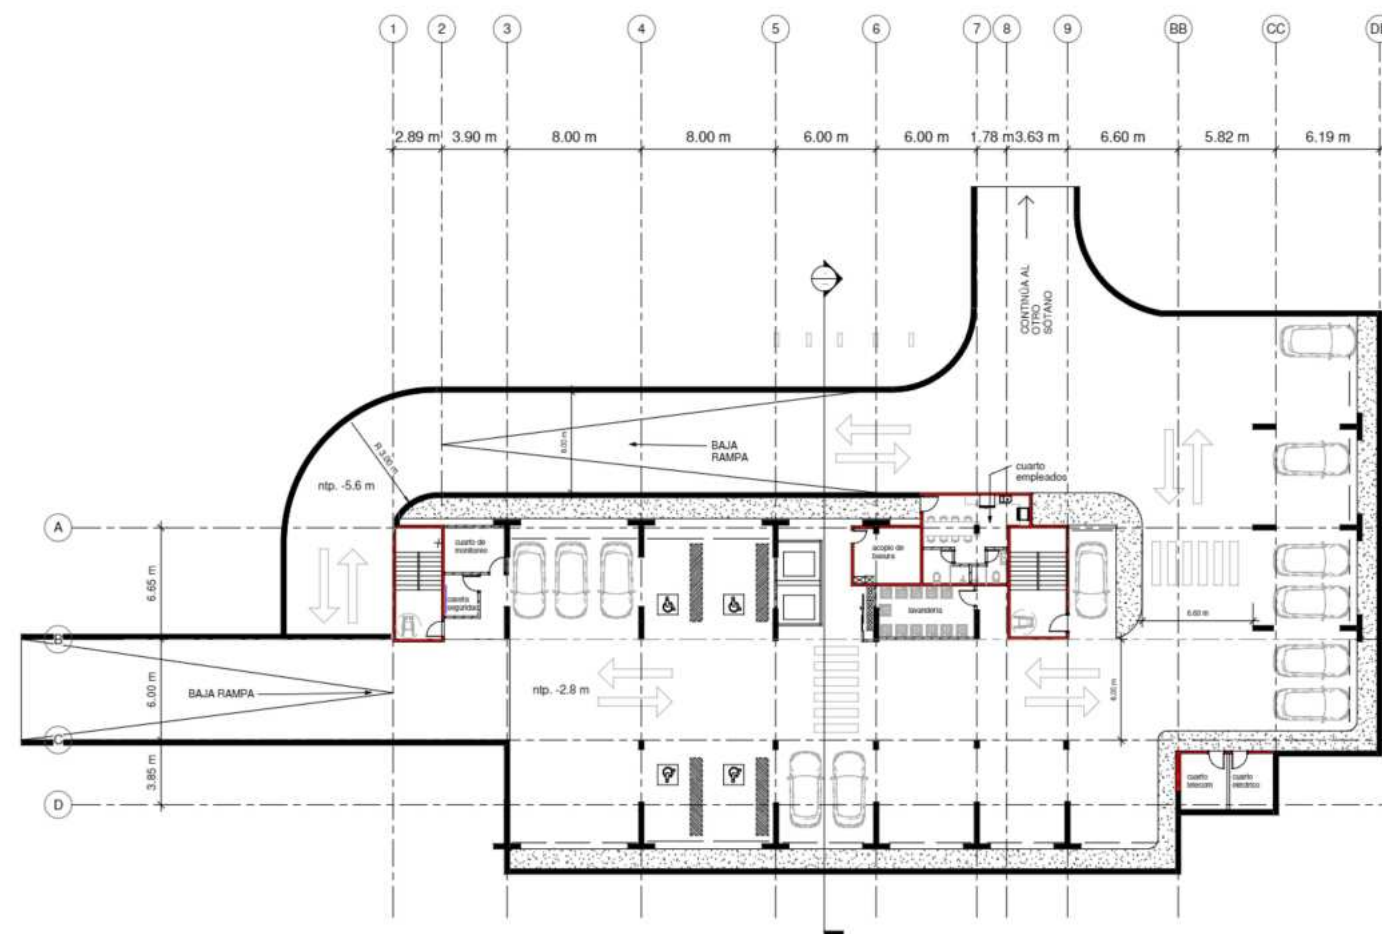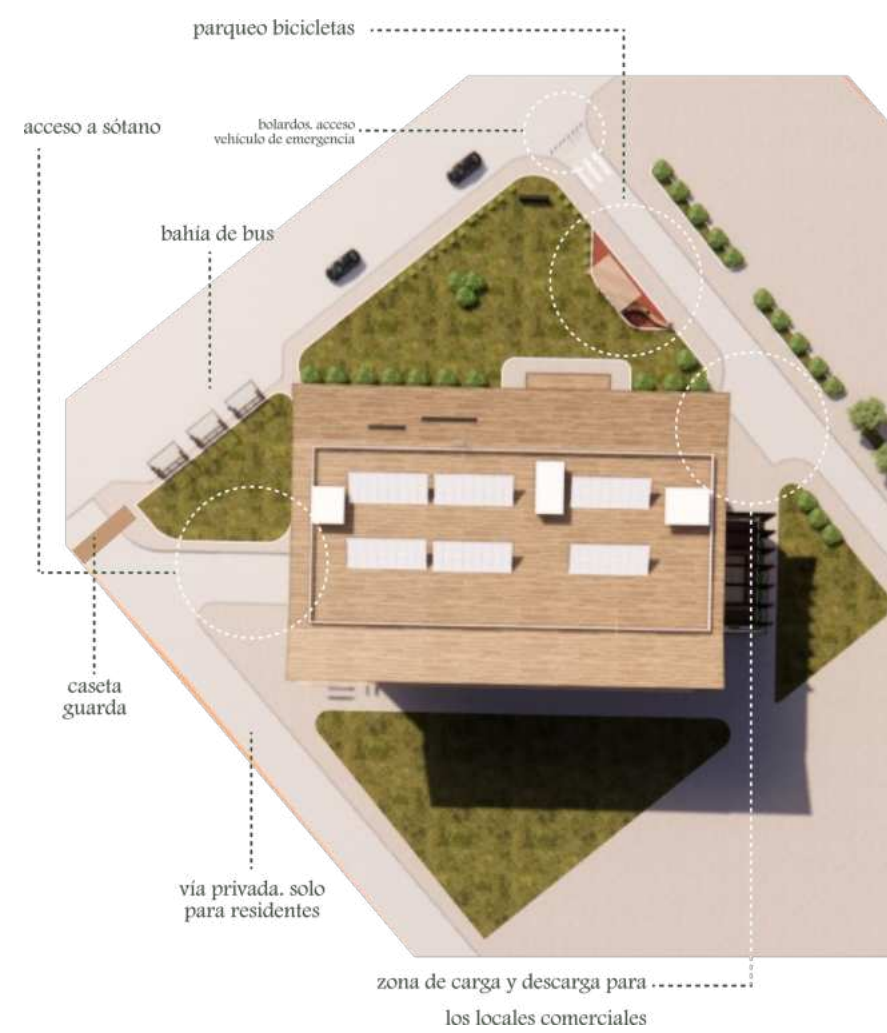

Sótano -1  
esc. 1:150

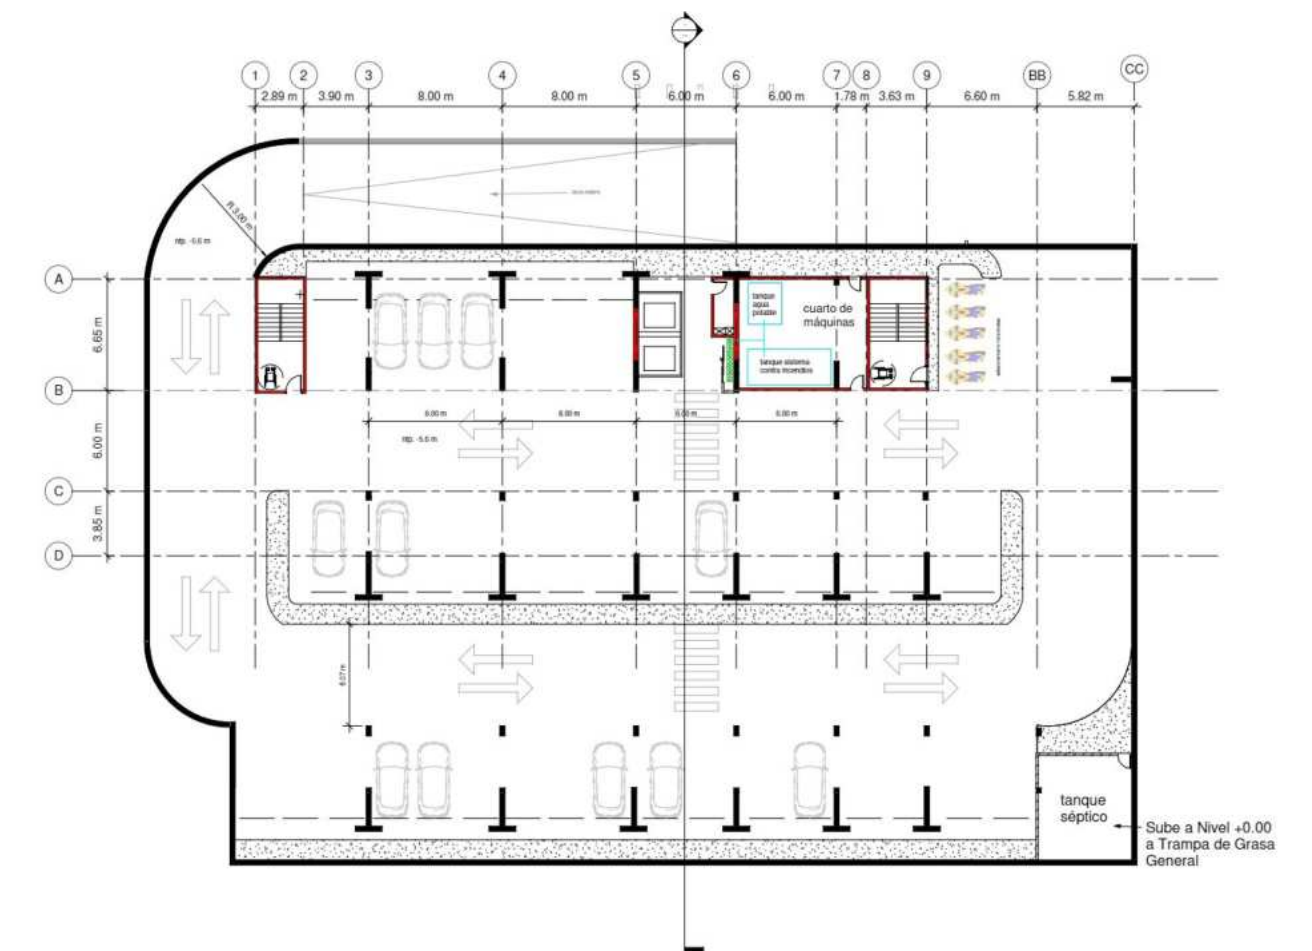

Sótano -2  
esc. 1:150

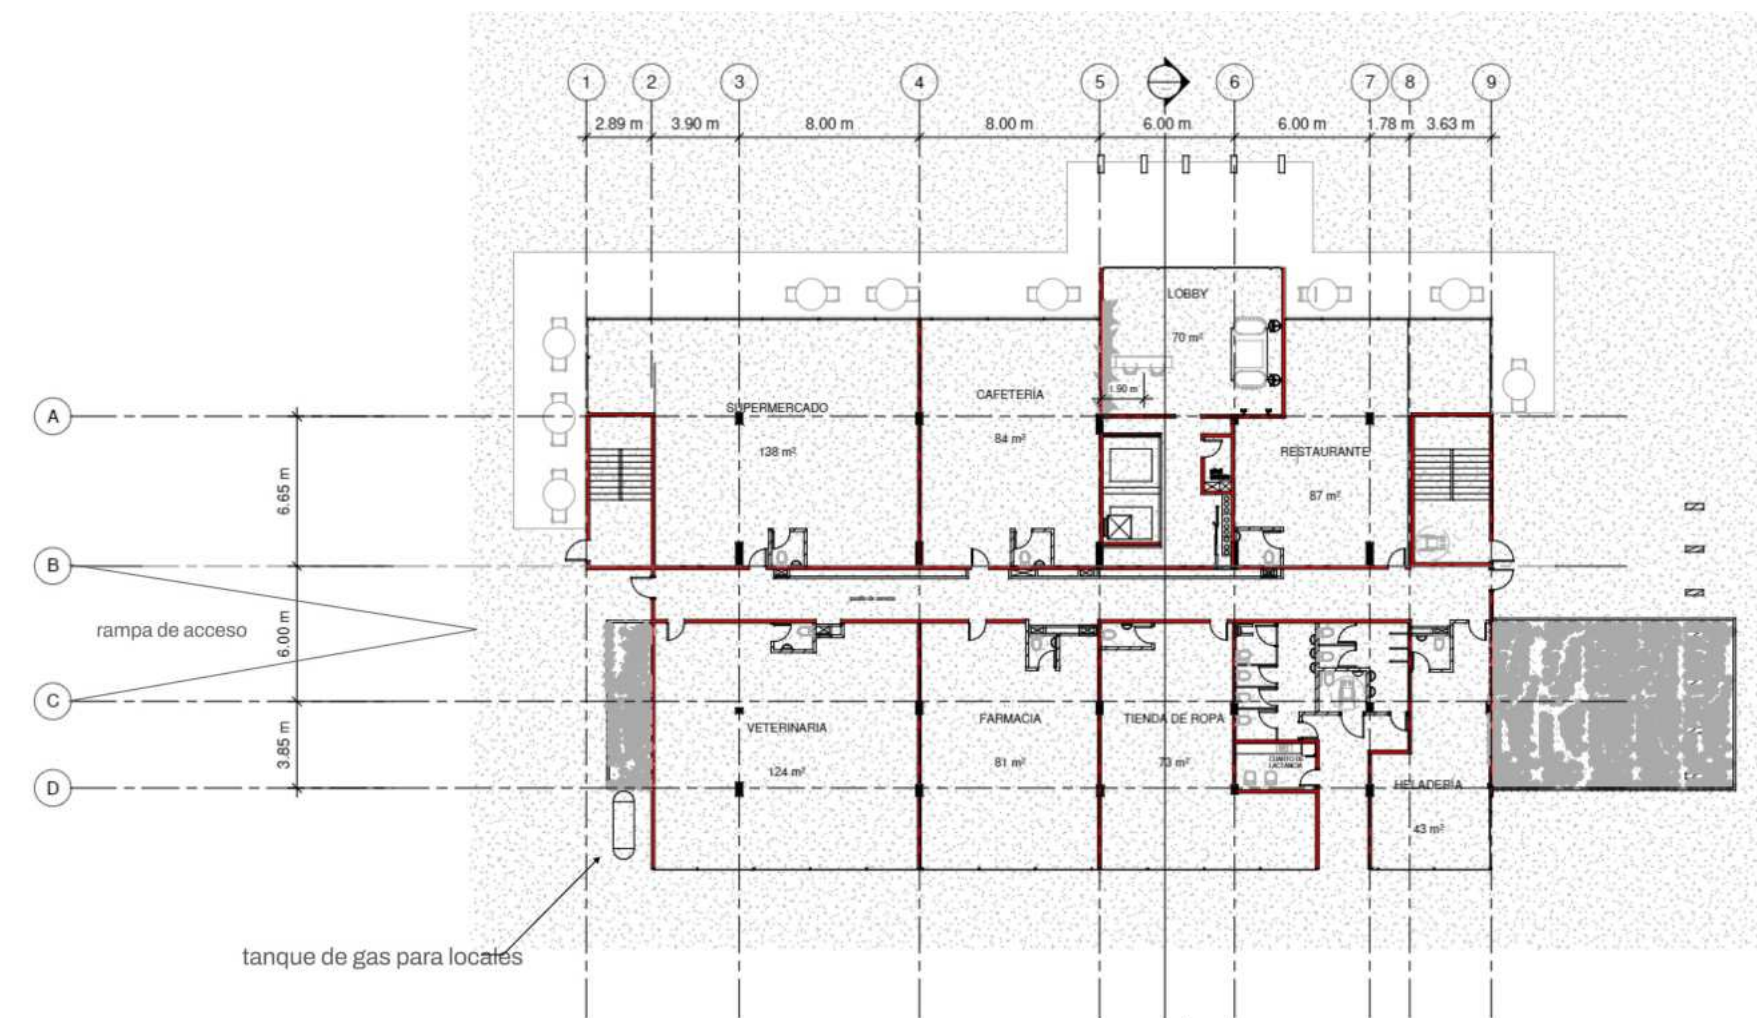

Planta 1. Comercial  
esc. 1:150



Planta 3. Residencial  
esc. 1:150







Render Lobby




Render Apartamento 100m2

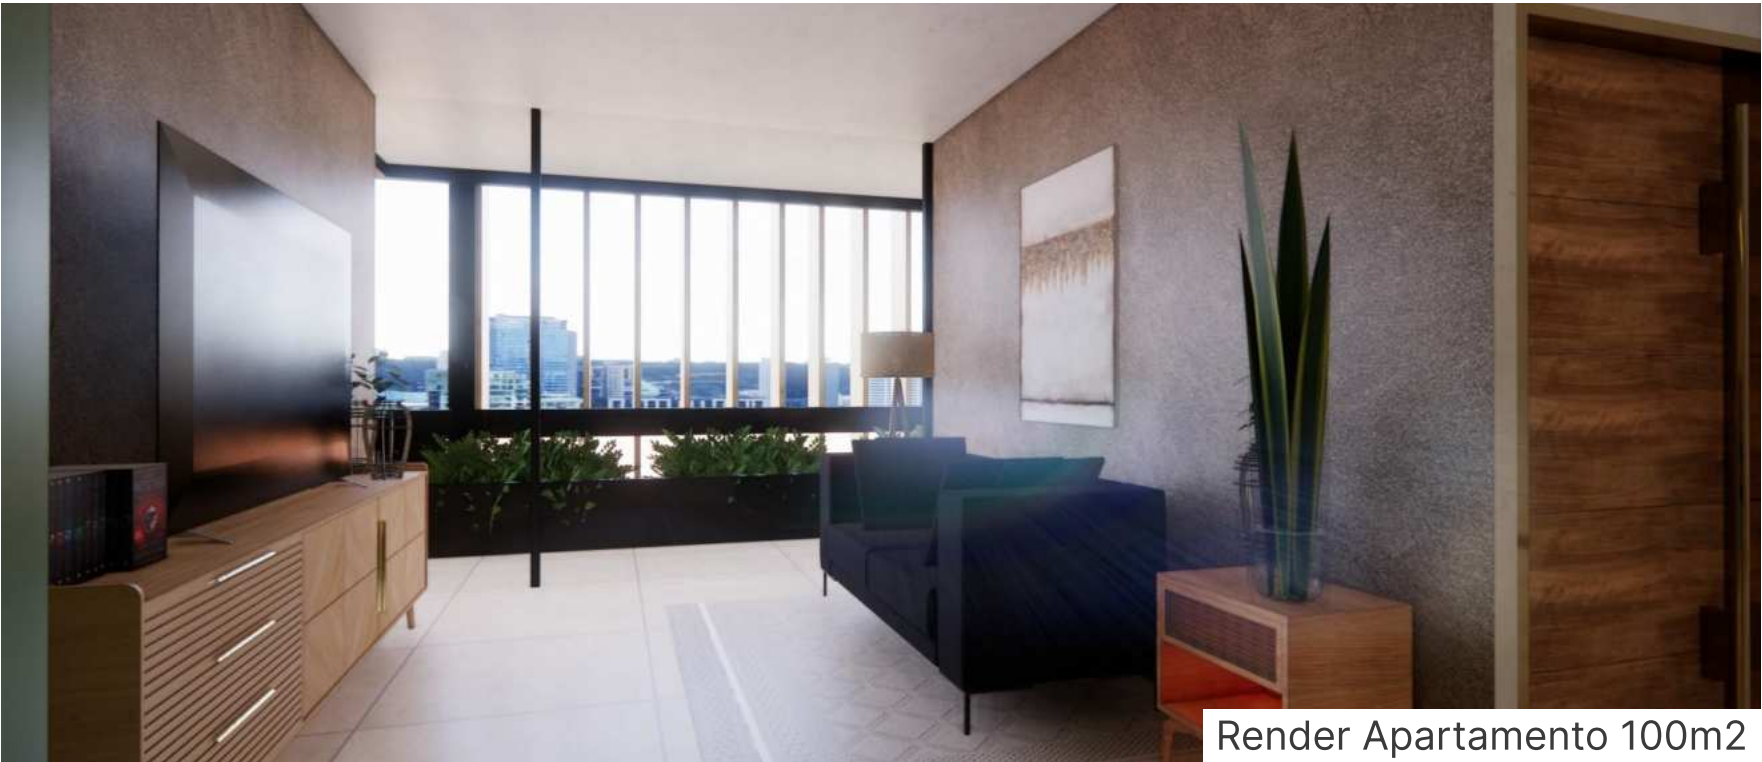

Render Apartamento 100m2

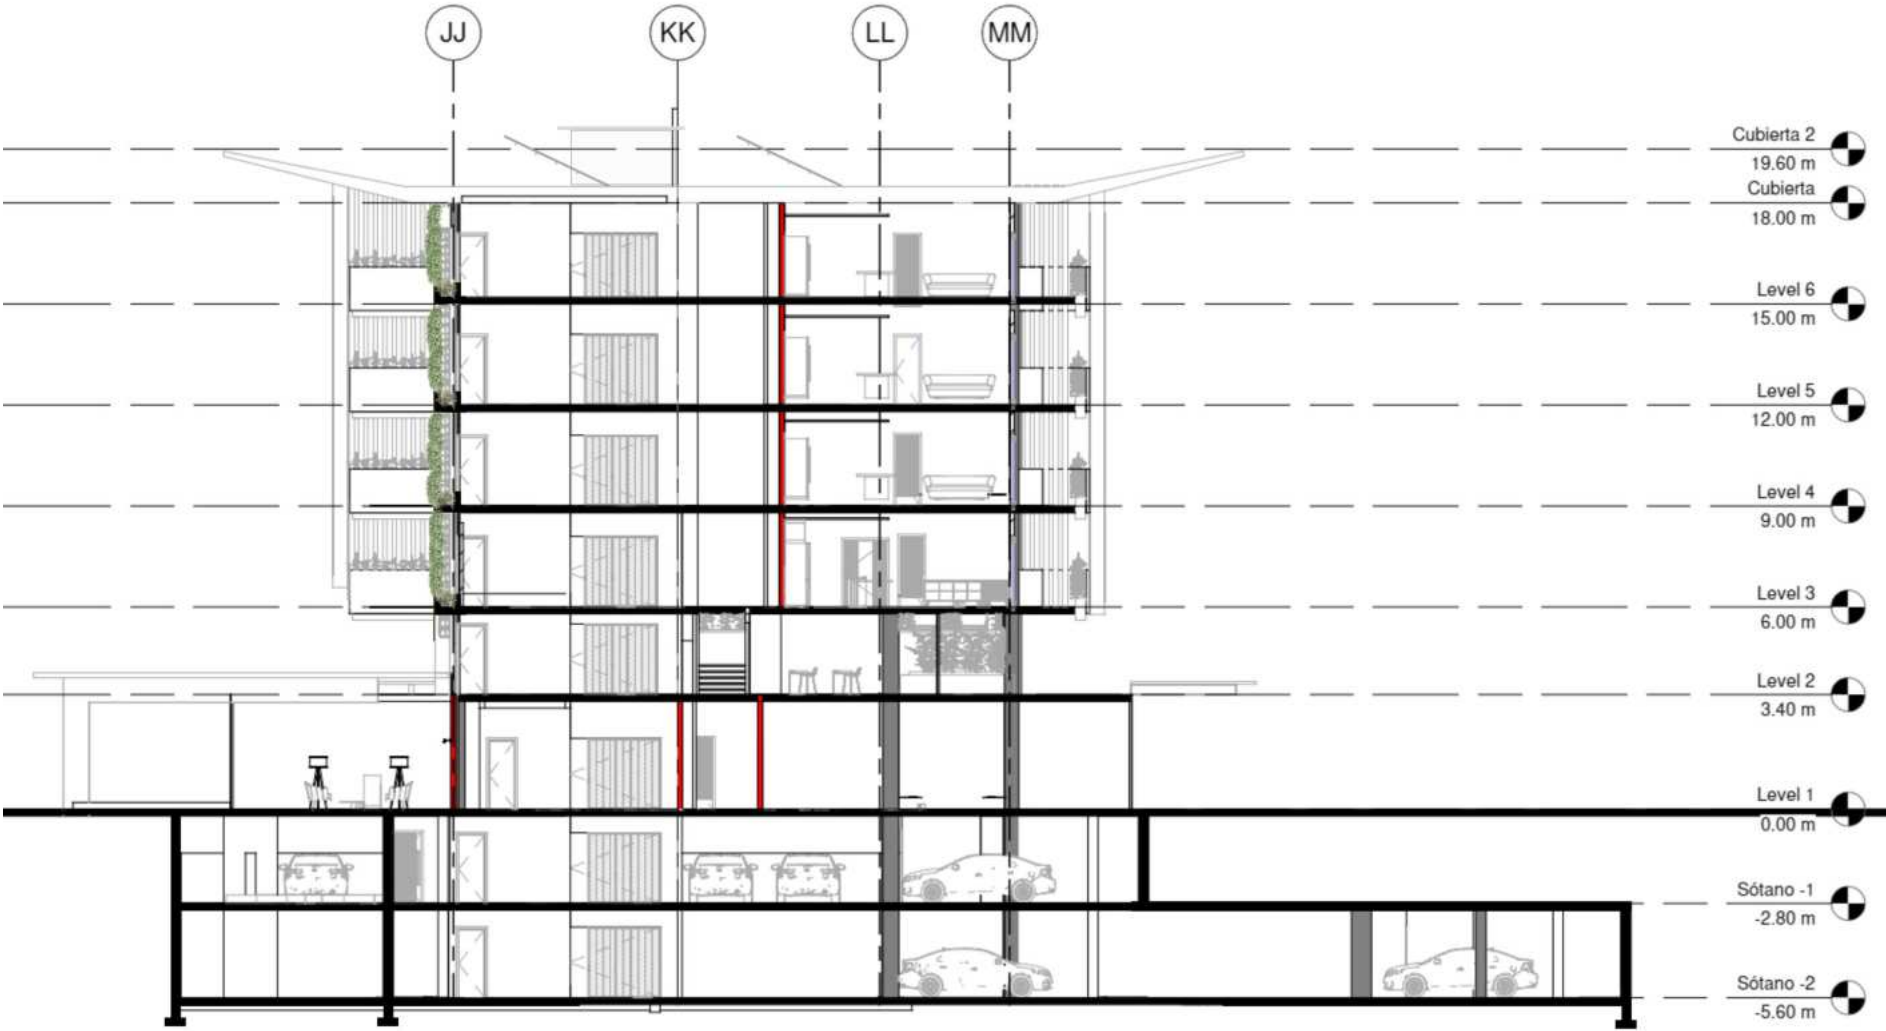

Sección transversal A-A  
esc. 1:150

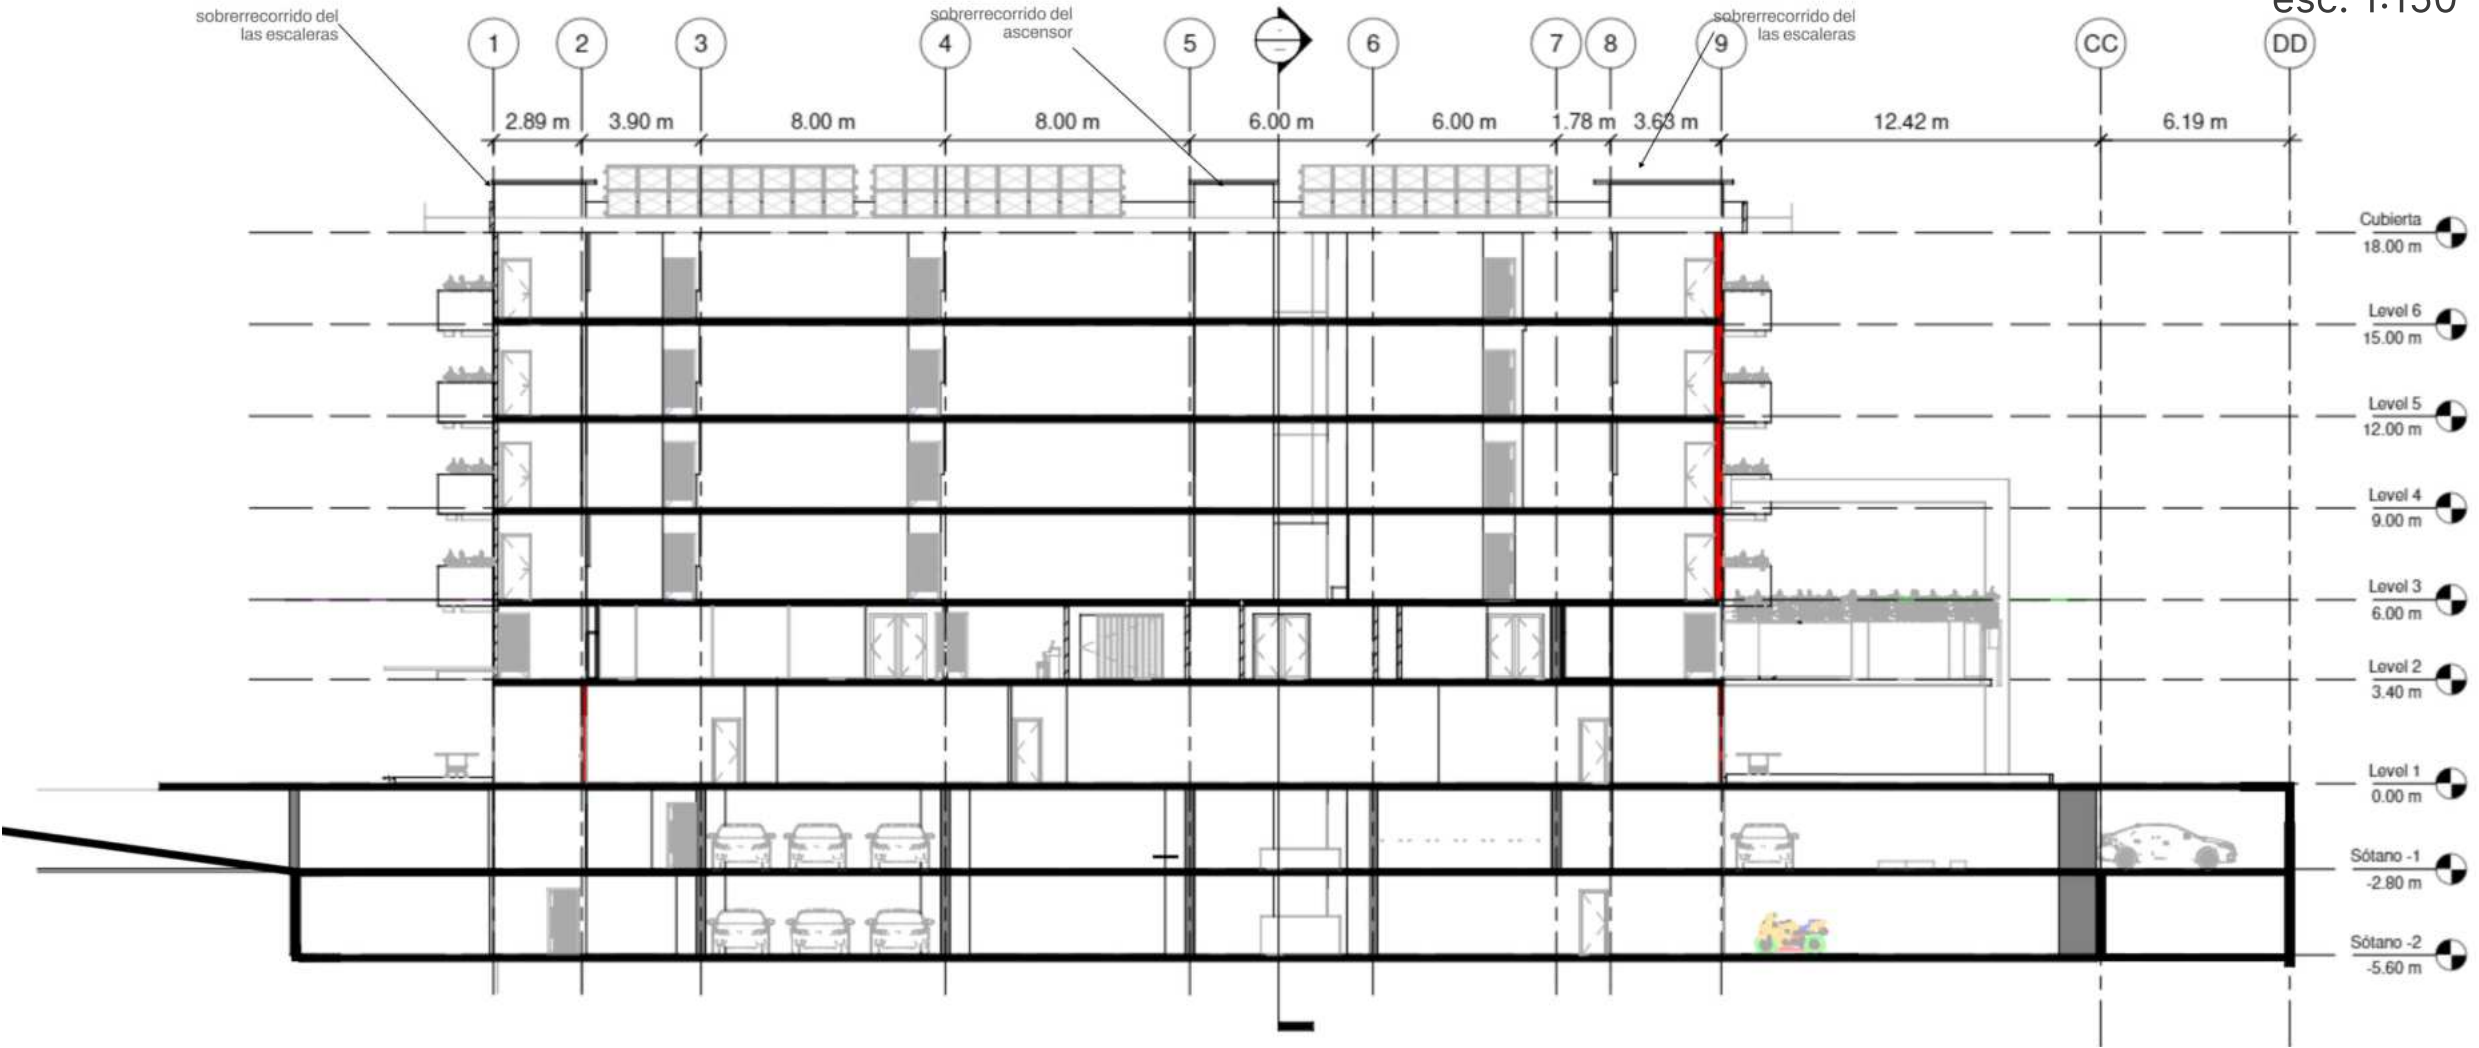

Sección longitudinal B-B  
esc. 1:150



# 02

## Entrelace Lúdico

Propuesta de diseño un cluster de 2 cuadras: Diseño de Coliving + Diseño de Hotel  
Taller 9




**Entrelace lúdico. A space for recreation and work release. To remain, to live together.**

The concept of the area to be intervened is located right in front of Ciudad Gobierno and next to the Pacific Train Station. The aim is for this space to be completely disconnected from work so that users can recreate, express themselves and share through playful, changing, dynamic spaces.

Therefore, the type of businesses used will be of great importance. The aim is to establish night markets (which extend the time slot of use), fairs, craft markets, stages for musical events, art galleries and spaces for just being, such as green areas, cafes...

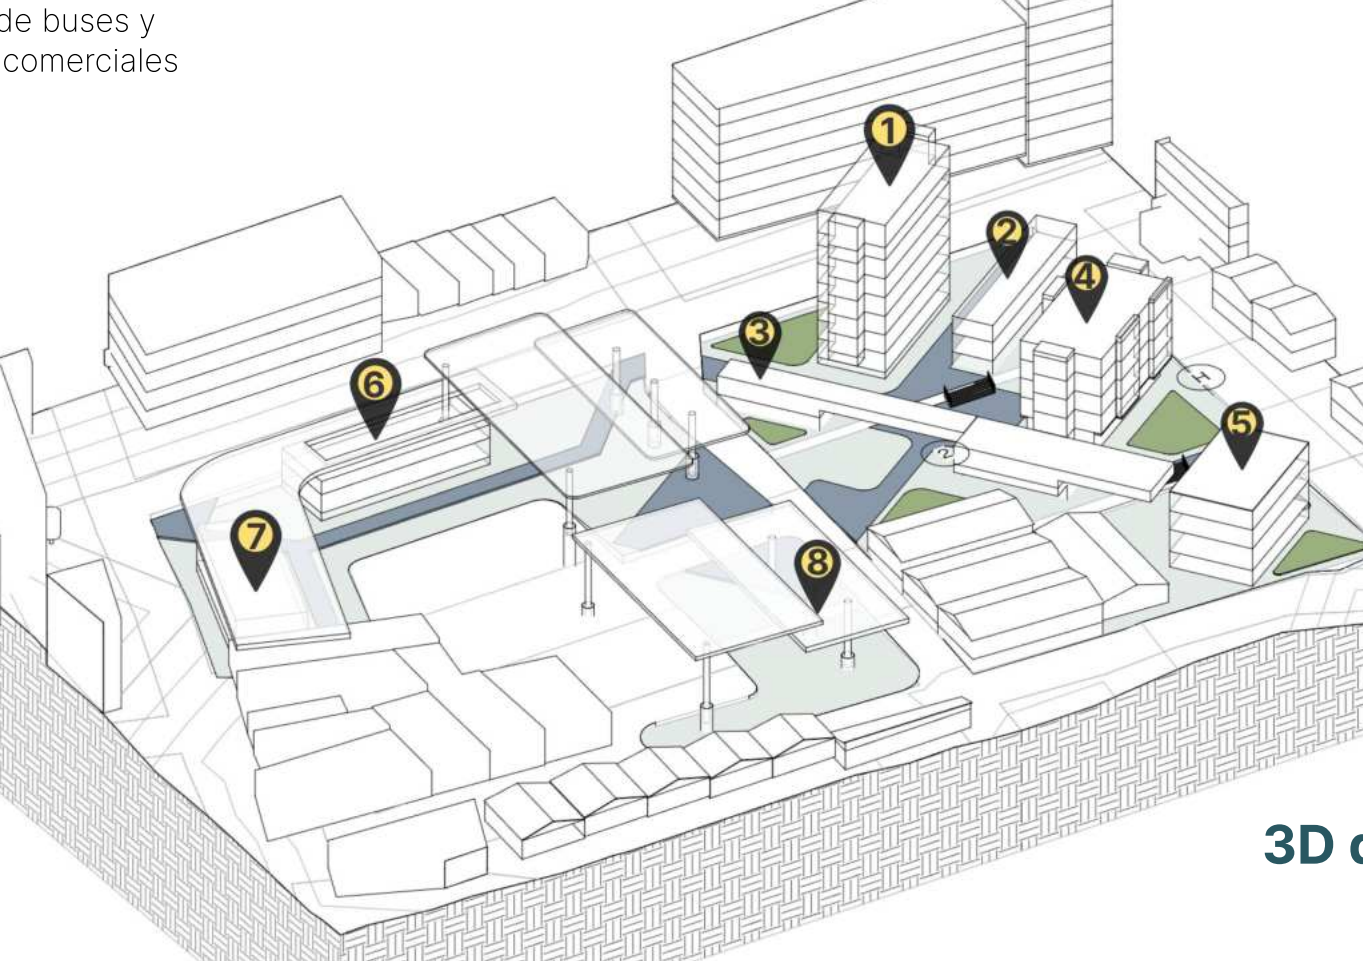


- 7 Locales comerciales
- 3 Terminal de buses y quioscos comerciales
- 
- 3D del clus  
compl**
- Se profundiza en el diseño del Hotel  
y del Coliving (1) así como los

Se profundiza en el diseño del Hotel (1) y del Coliving (4) así como los ejes comerciales (2) y (3)






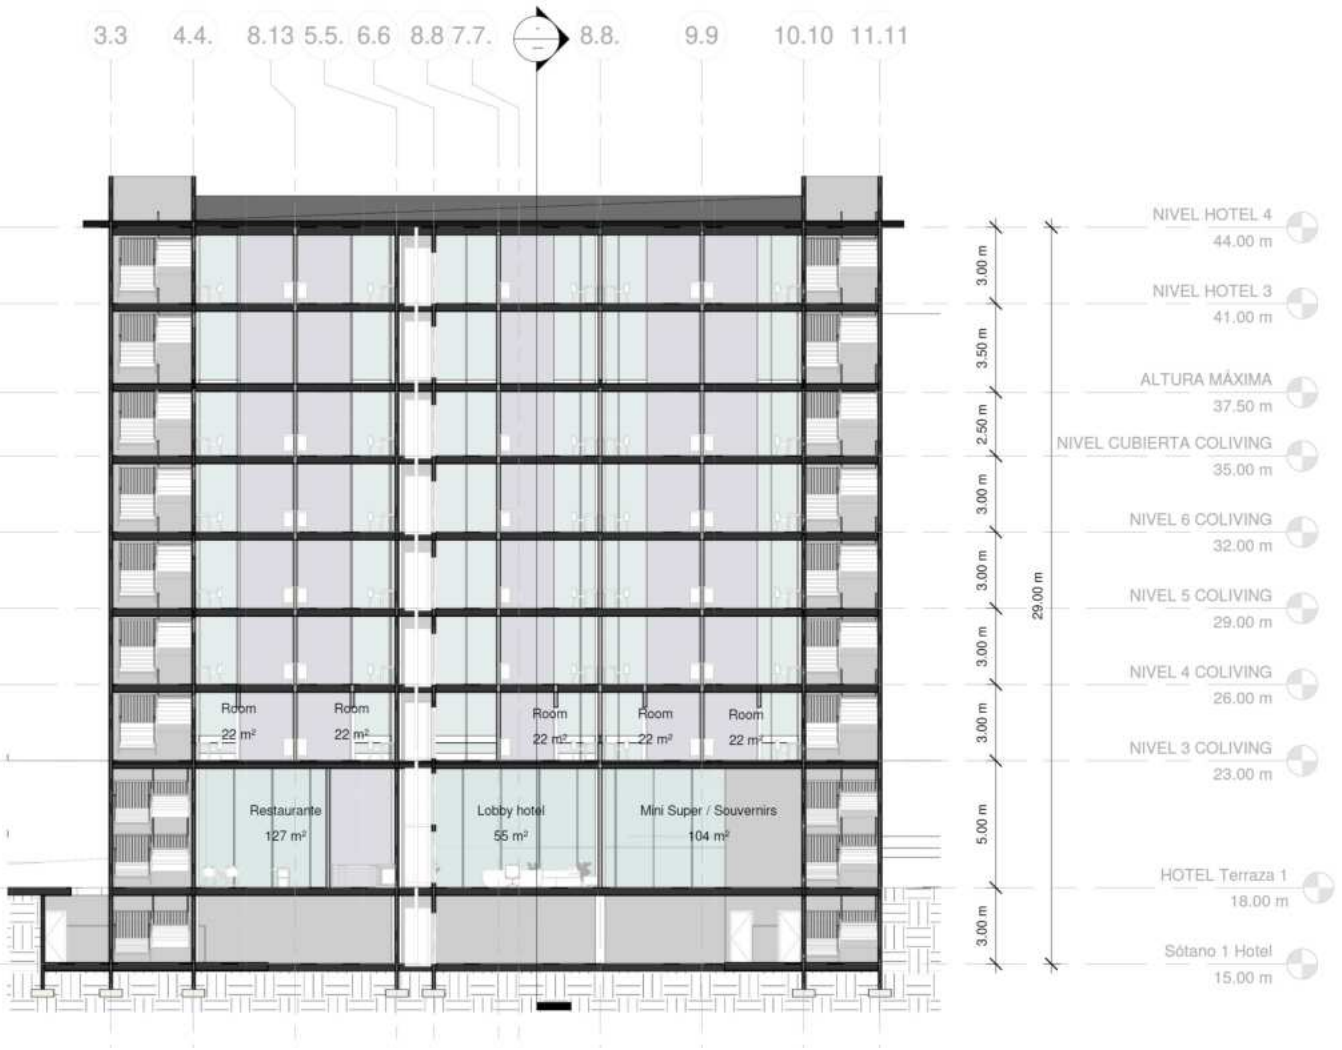


SECCIÓN LONGITUDINAL DEL HOTEL



SECCIÓN TRANSVERSAL DEL HOTEL

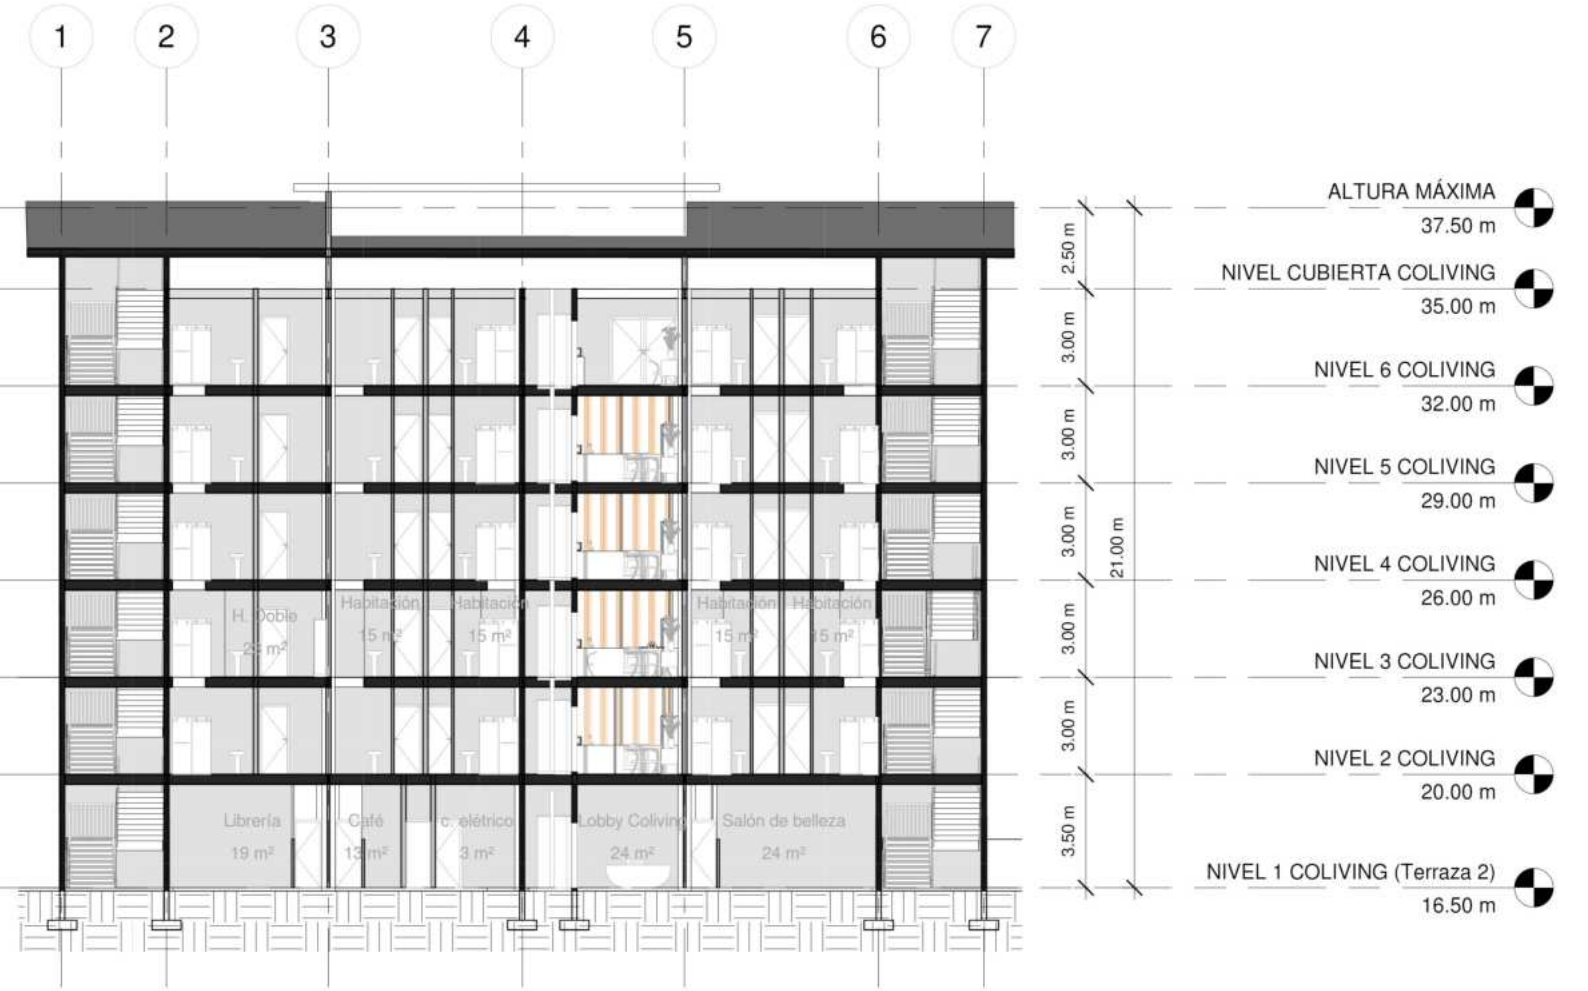

SECCIÓN LONGITUDINAL DEL COLIVING

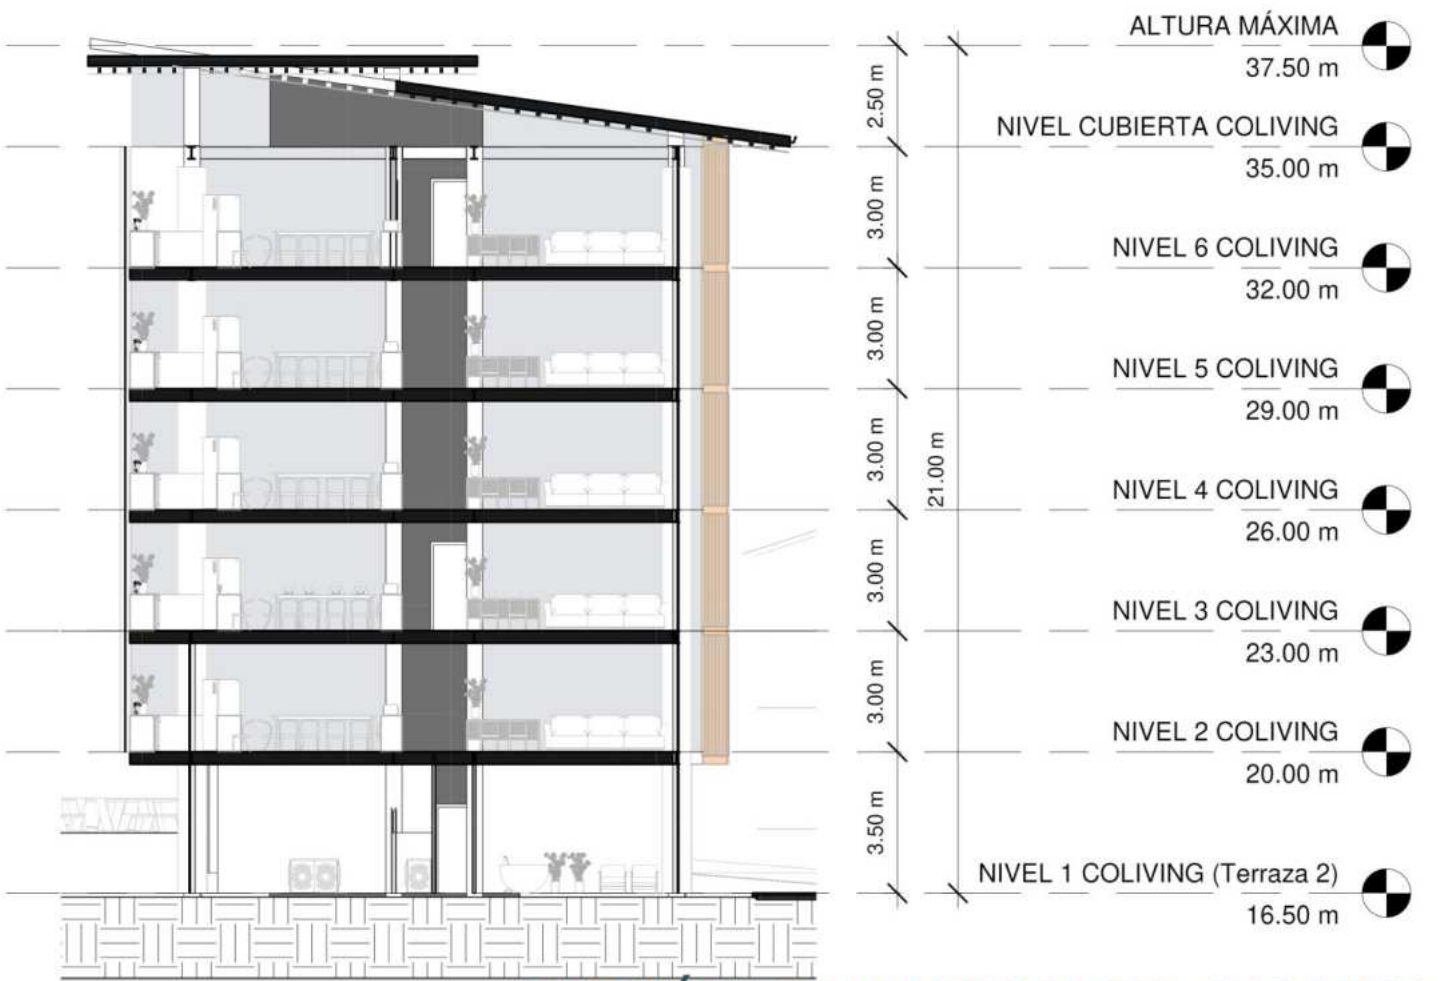

SECCIÓN TRANSVERSAL DEL COLIVING



# 03

## Museo del Trópico


Propuesta de diseño de un museo en la zona de Jacó, Puntarenas  
Taller 6




The Tropic Museum in Jacó seeks to be a **space destined to tell the story of the climatic biodiversity of Costa Rica**, through a route that goes from the entrance of Jacó to the beach, generating a **journey** that is enjoyed throughout the entire museum.

The tropical museum seeks more than just being a museum, but a place where the experience of visiting Jacó can be lived along with its **local culture**. The aim is to create spaces for socialization and integration, where from young people to **older adults** can coexist at the same point, these being the priority, which is why benches with shade are placed at all points for the comfort of this population.




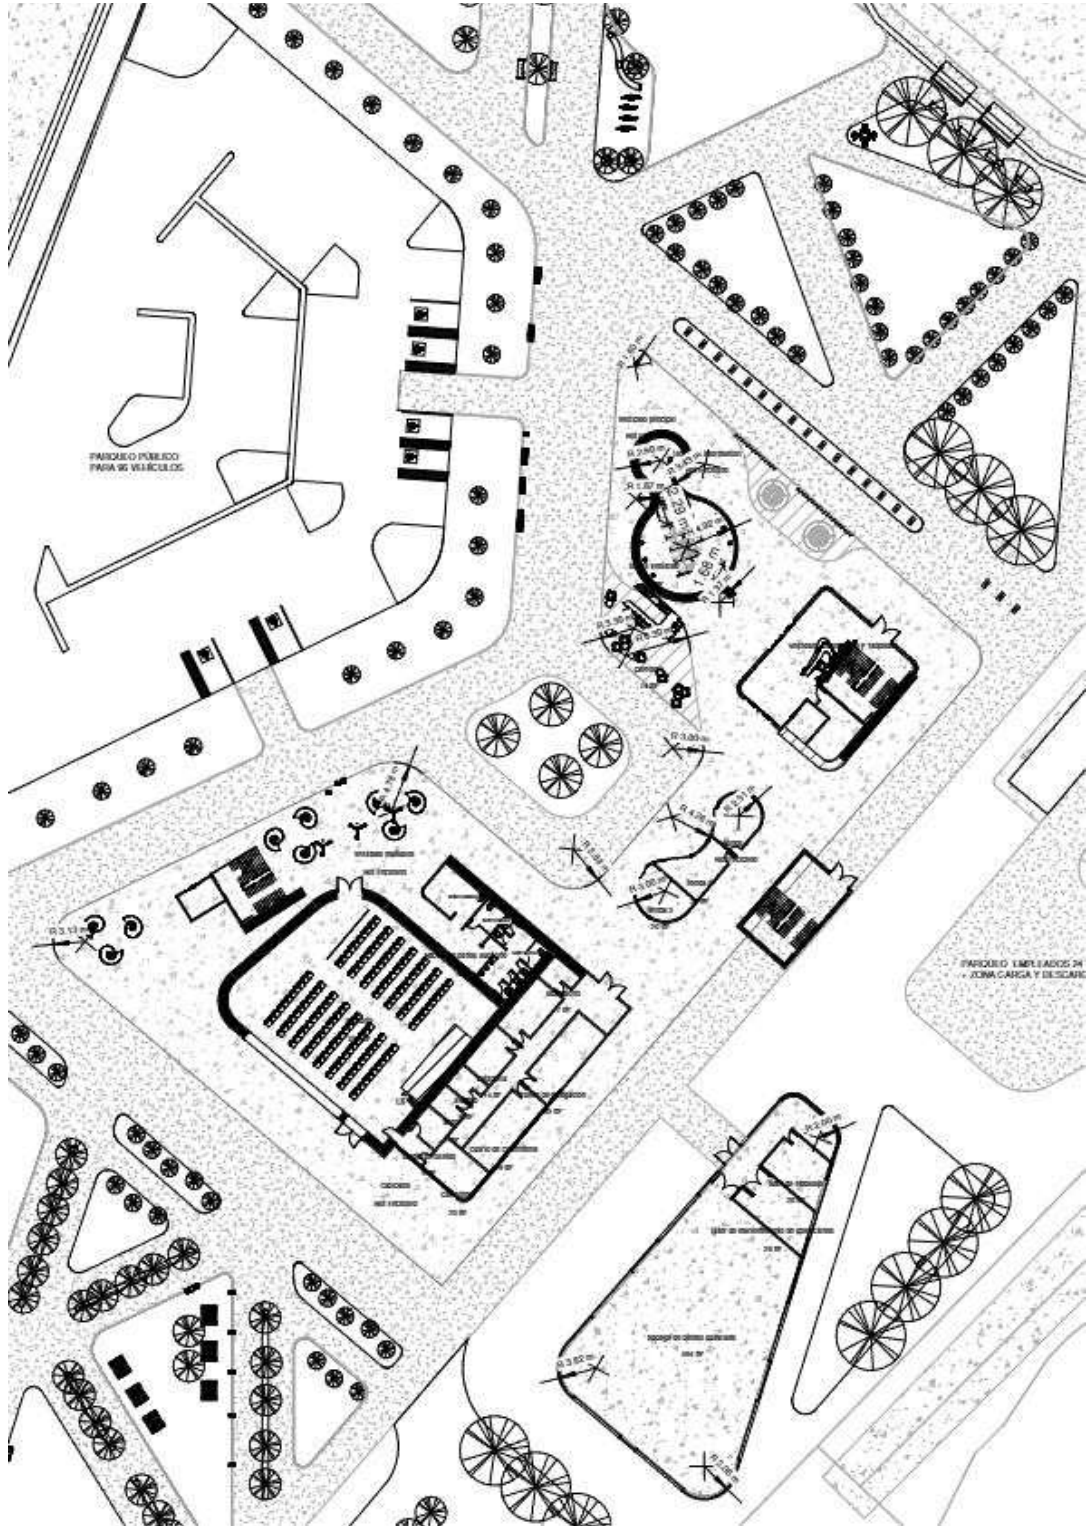


Planta arquitectónica Nivel 1  
esc. 1:150

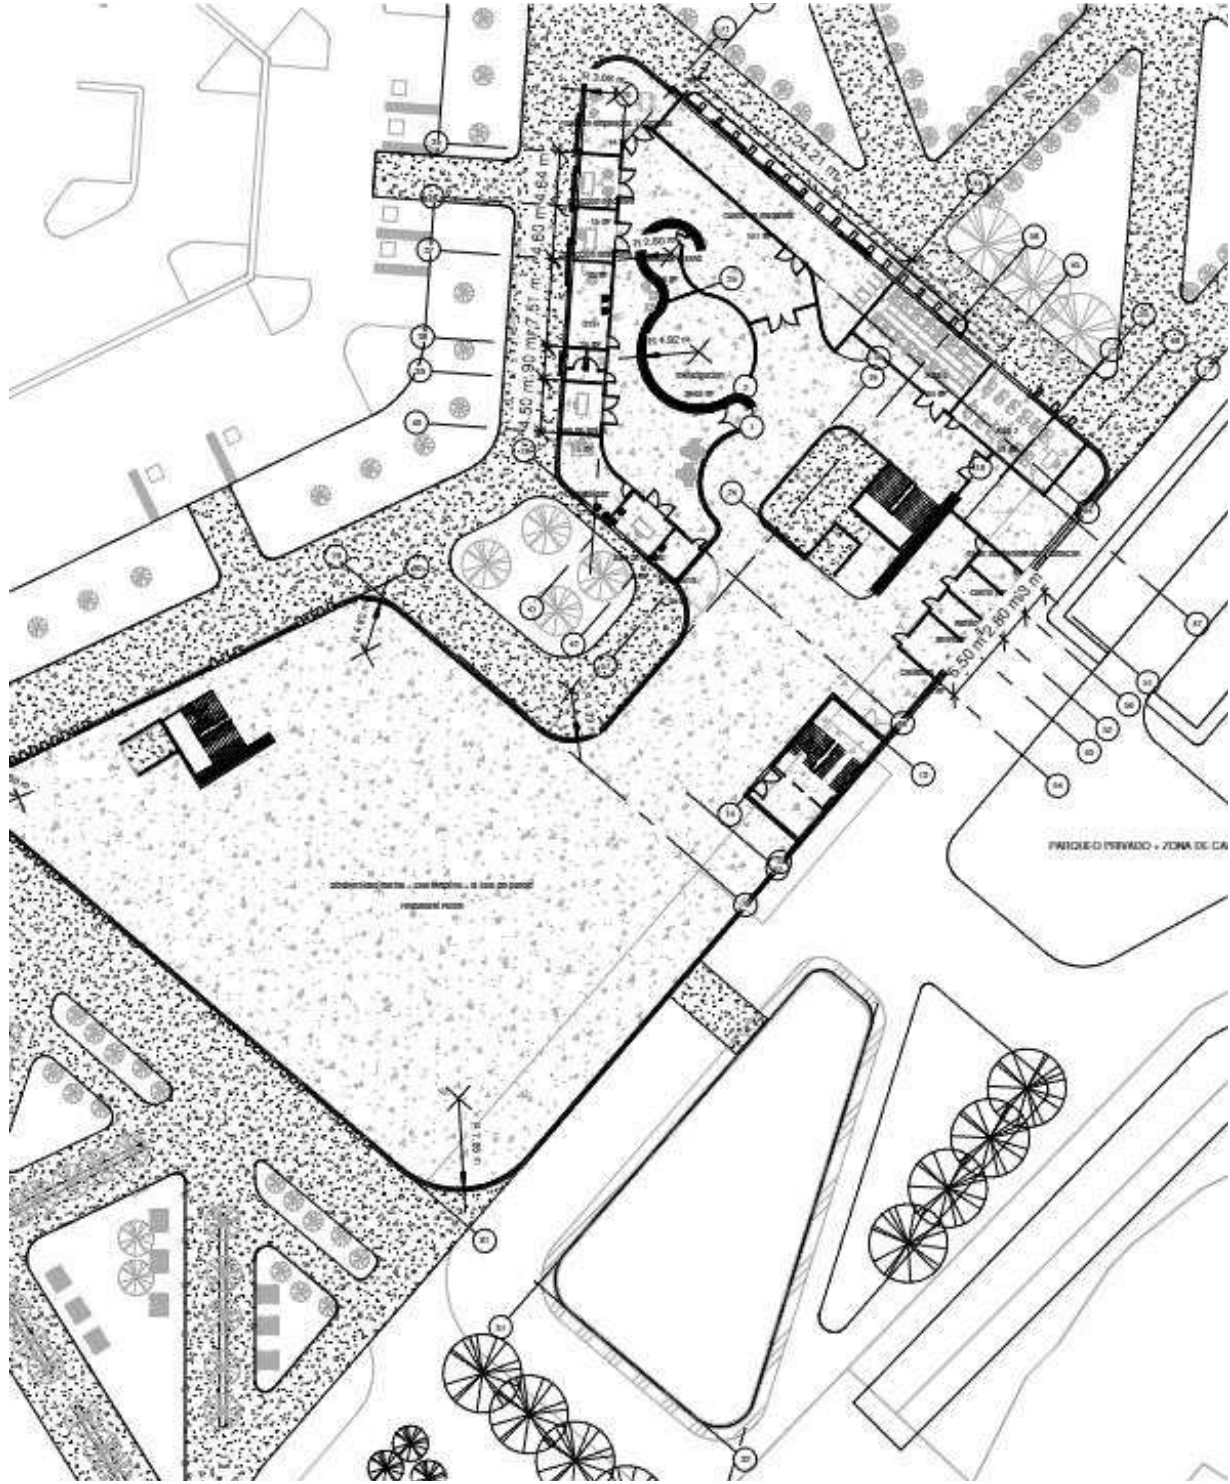

Planta arquitectónica Nivel 2  
esc. 1:150

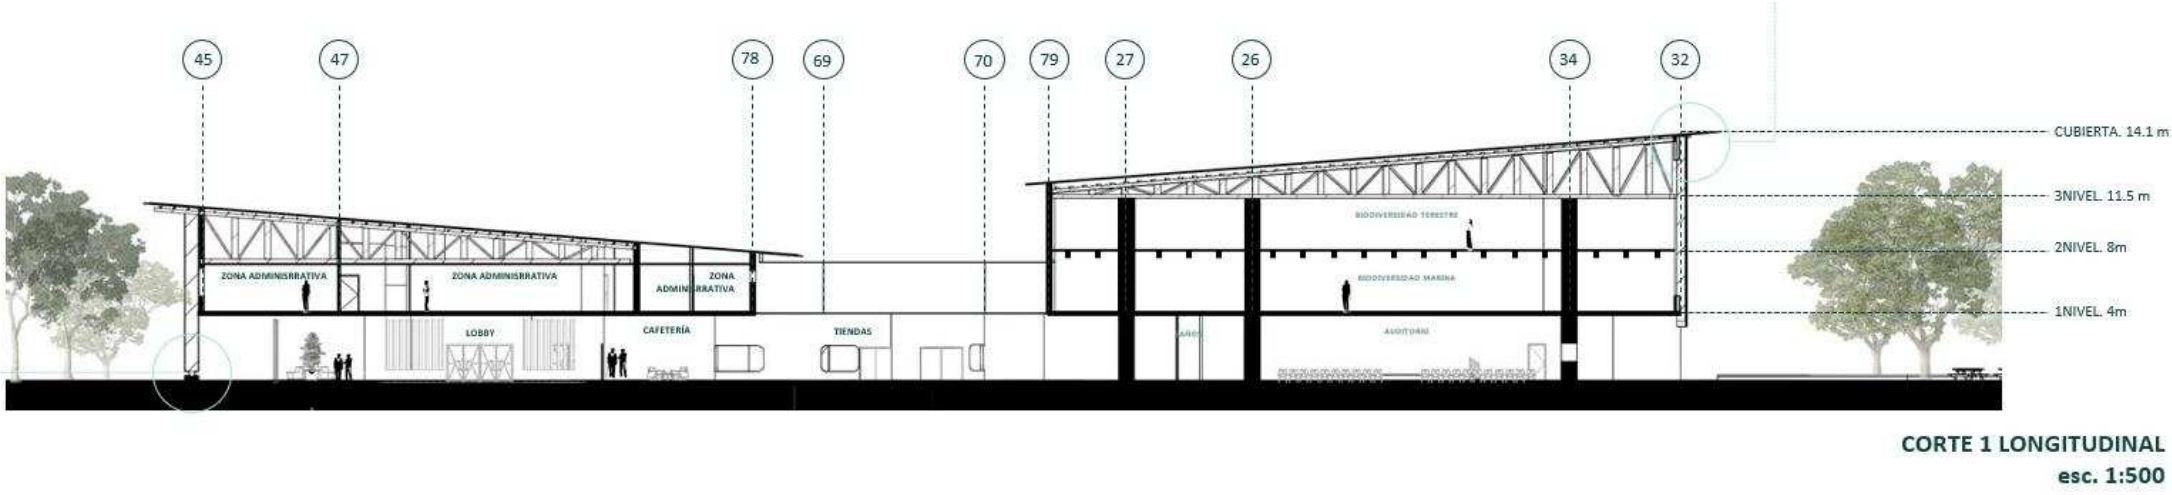


CORTE 1 LONGITUDINAL  
esc. 1:500

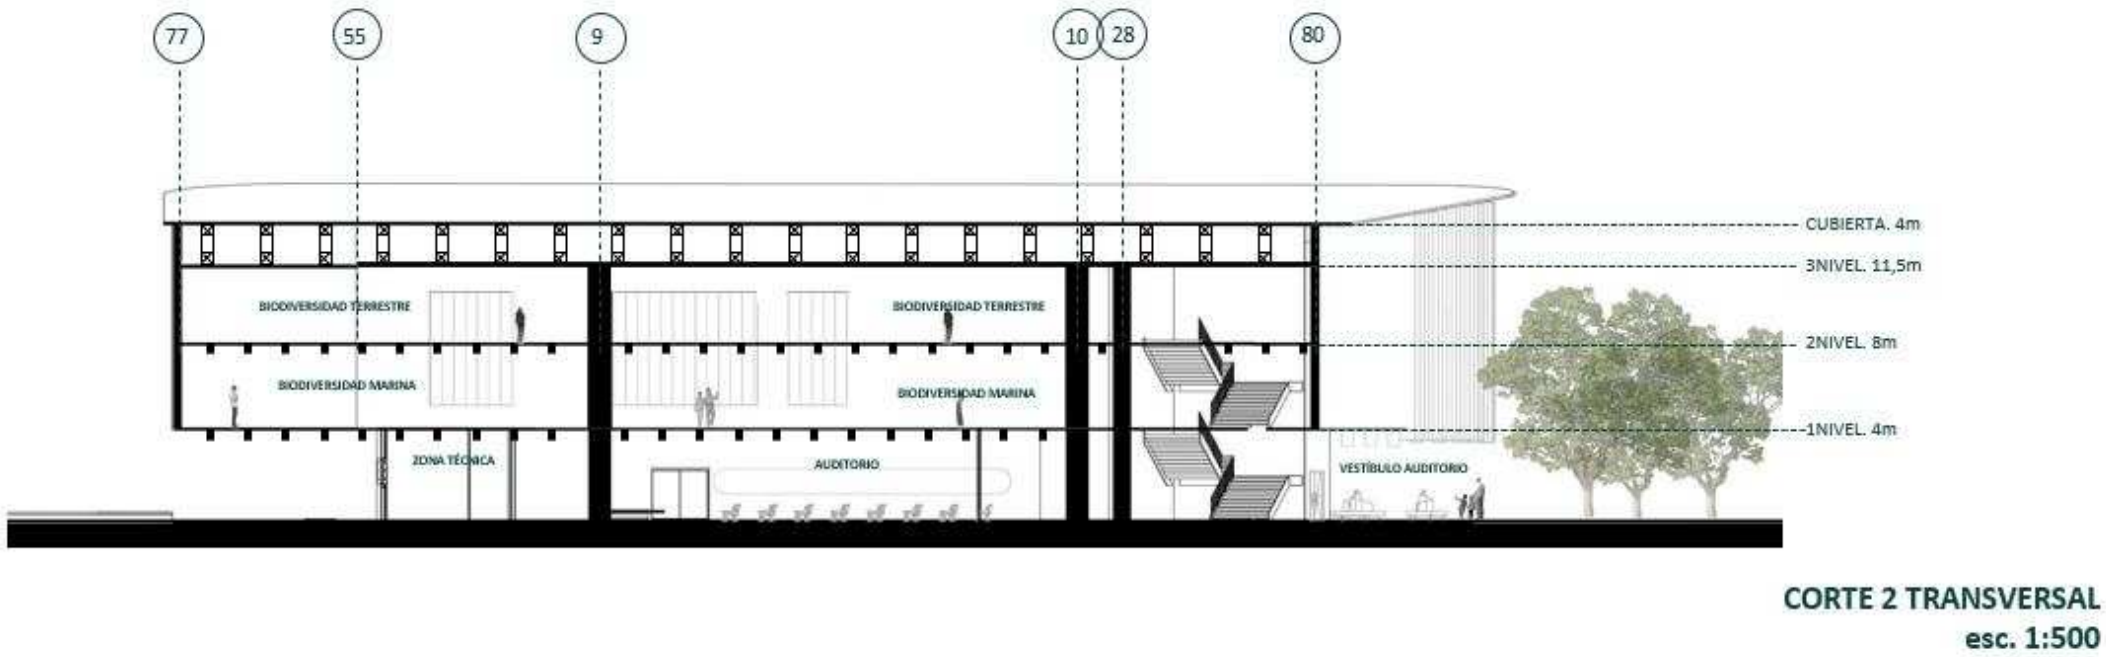

CORTE 2 TRANSVERSAL  
esc. 1:500






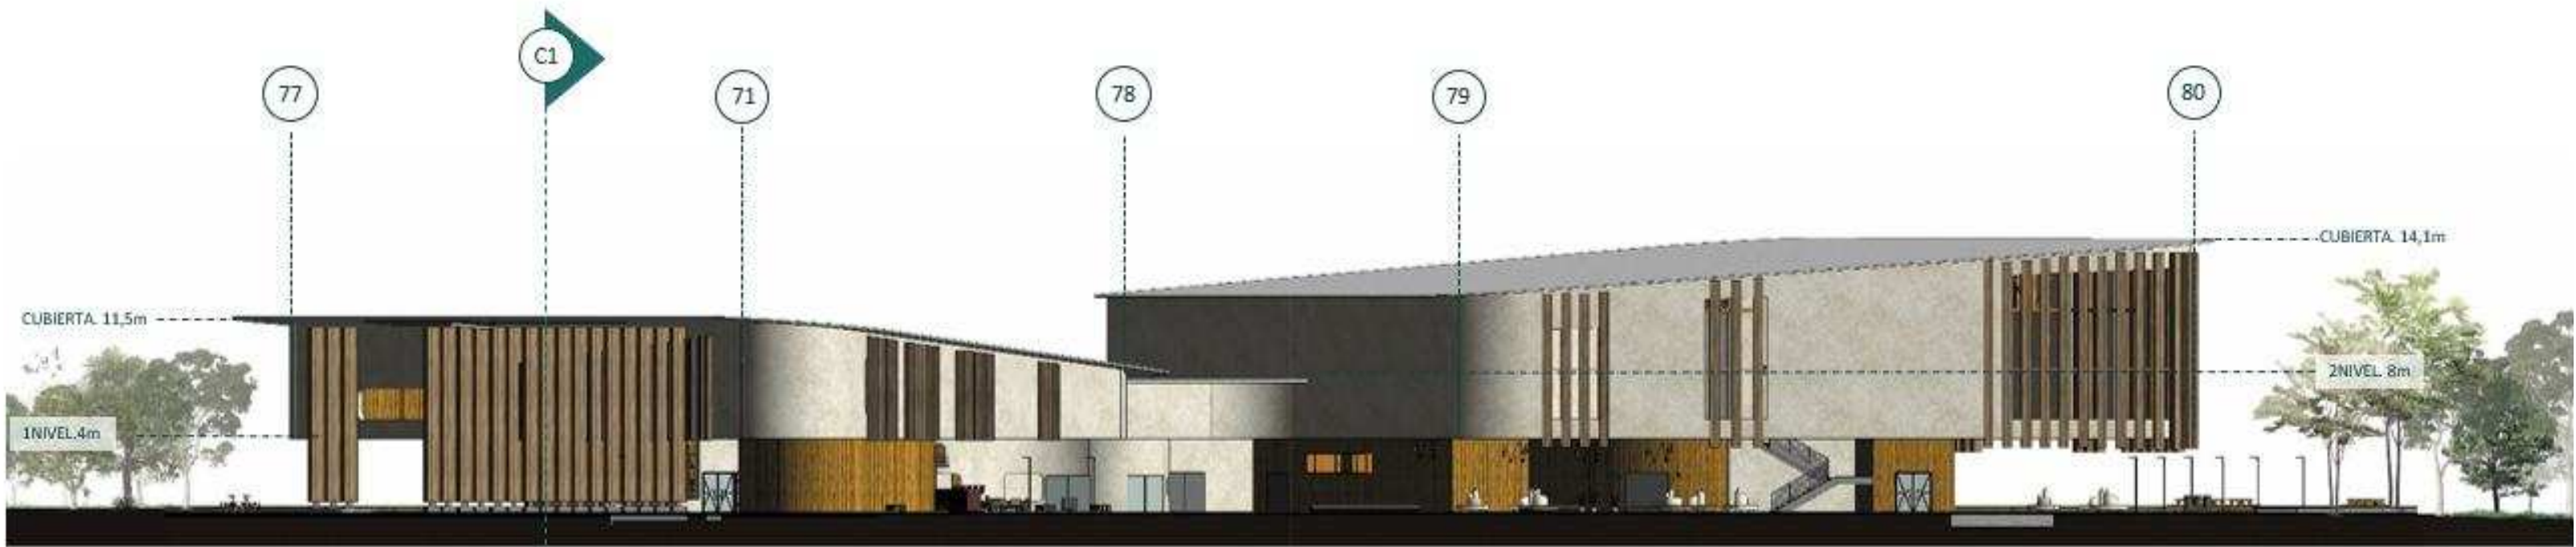

ELEVACIÓN OESTE  
Esc. 1:250

Esc. 1:250

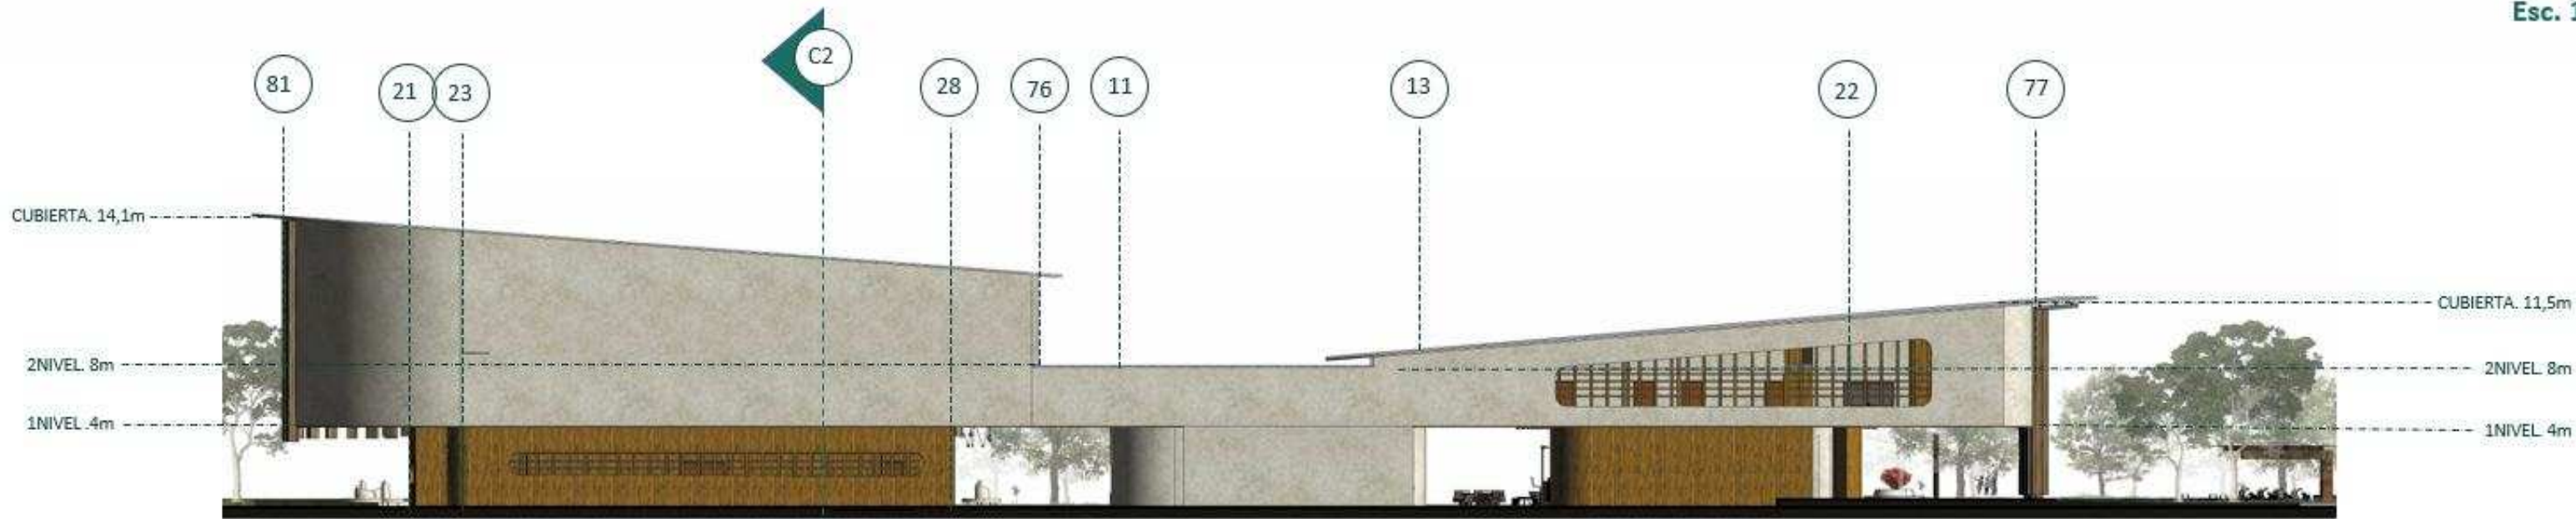

ELEVACIÓN ESTE  
Esc. 1:250



# 04

## Residencias Hogar del Jardín

Propuesta de diseño de un centro geriátrico para la zona de Loyola, Cartago  
Taller 8



## RESIDENCIAS hogar del jardín

Hogar del Jardín residences seek to be a suitable space with high comfort and luxury for older adults. For this project, the understanding of the country's law 7600 was prioritized, as well as other extra requirements for the comfort of the elderly.

The project has a residential area, health area, multipurpose rooms with a dining room and among other spaces.



todas las cotas se indican  
en los acercamientos de las  
plantas\*



## PROGRAMA






Render sala común




Render rampa




Render plaza central

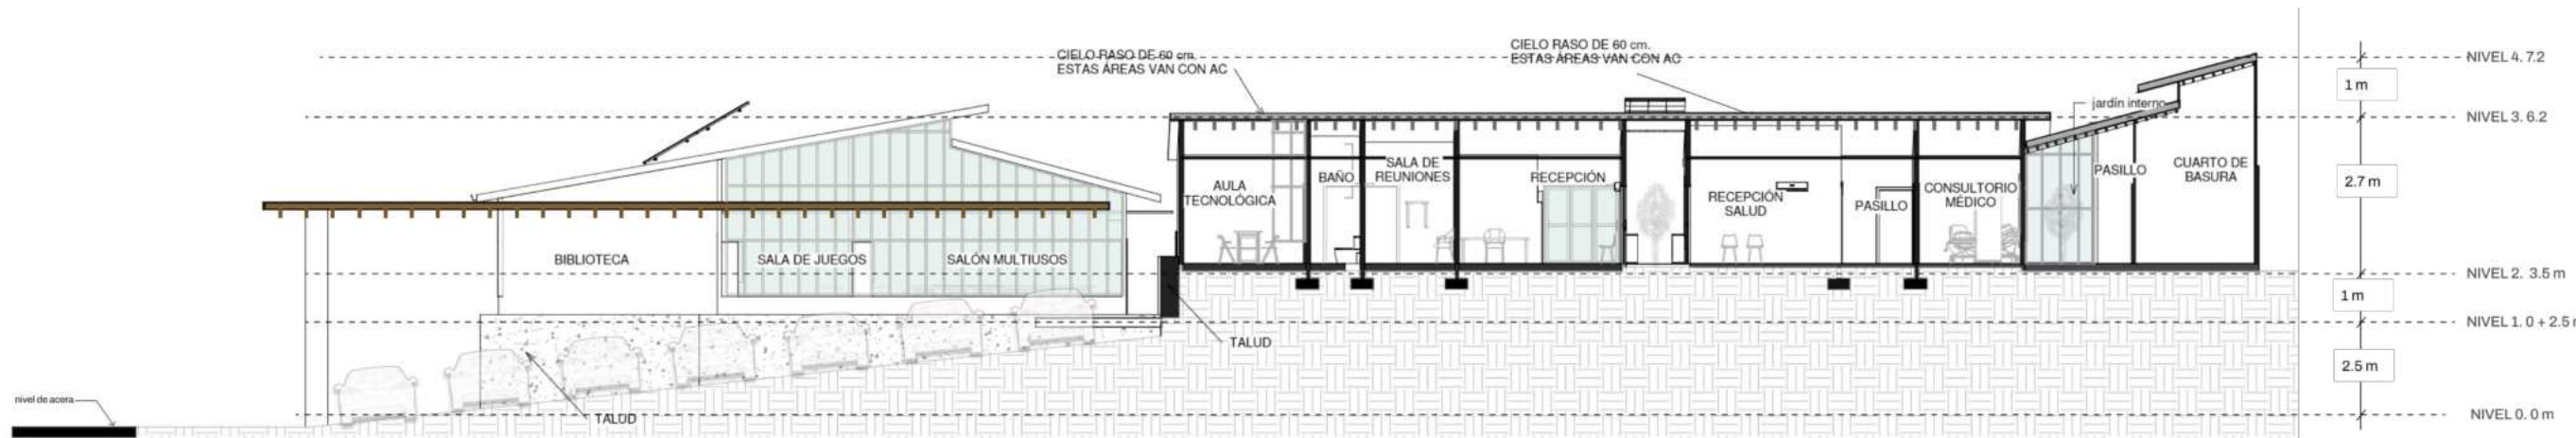


SECCIÓN A-A  
esc 1:100

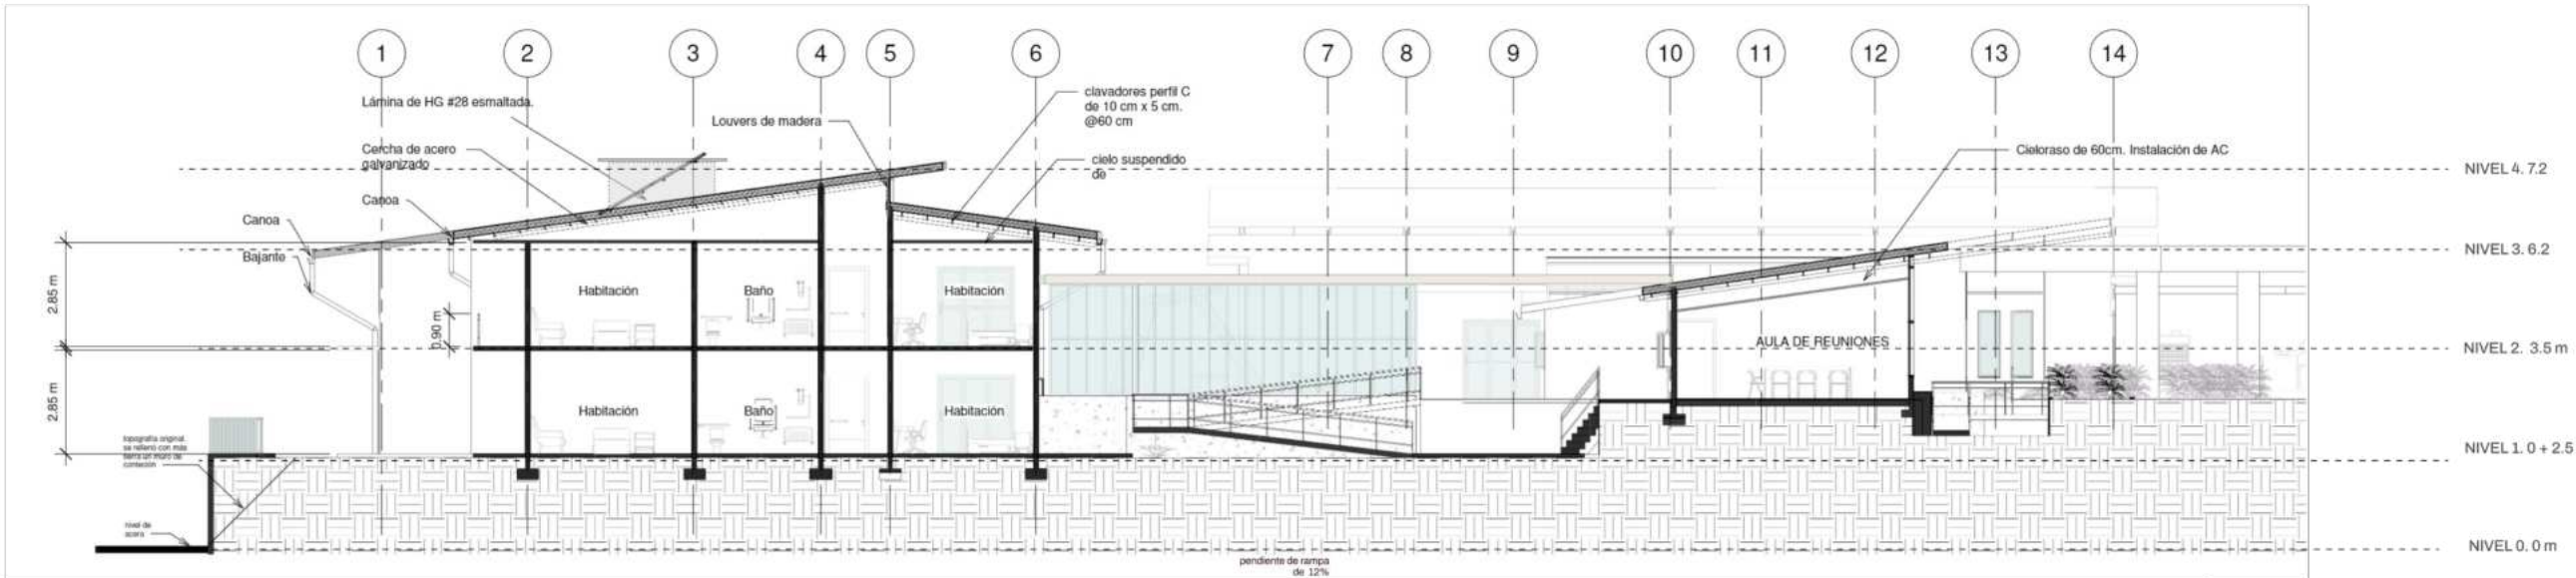

SECCIÓN B-B  
esc 1:100











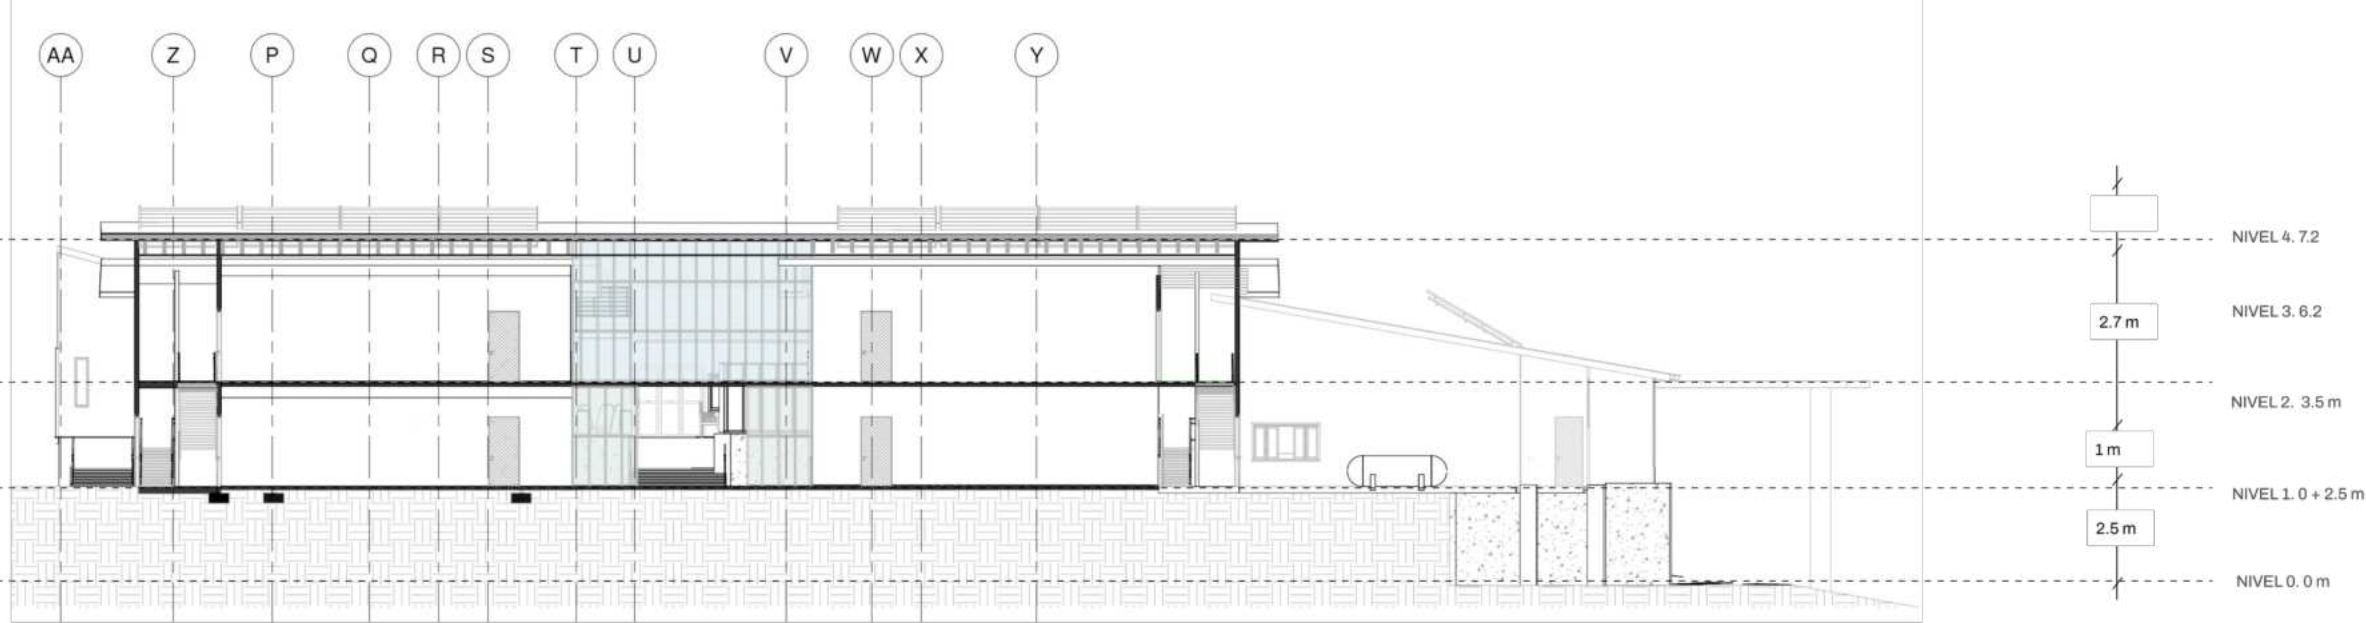


SECCIÓN C-C  
esc 1:100

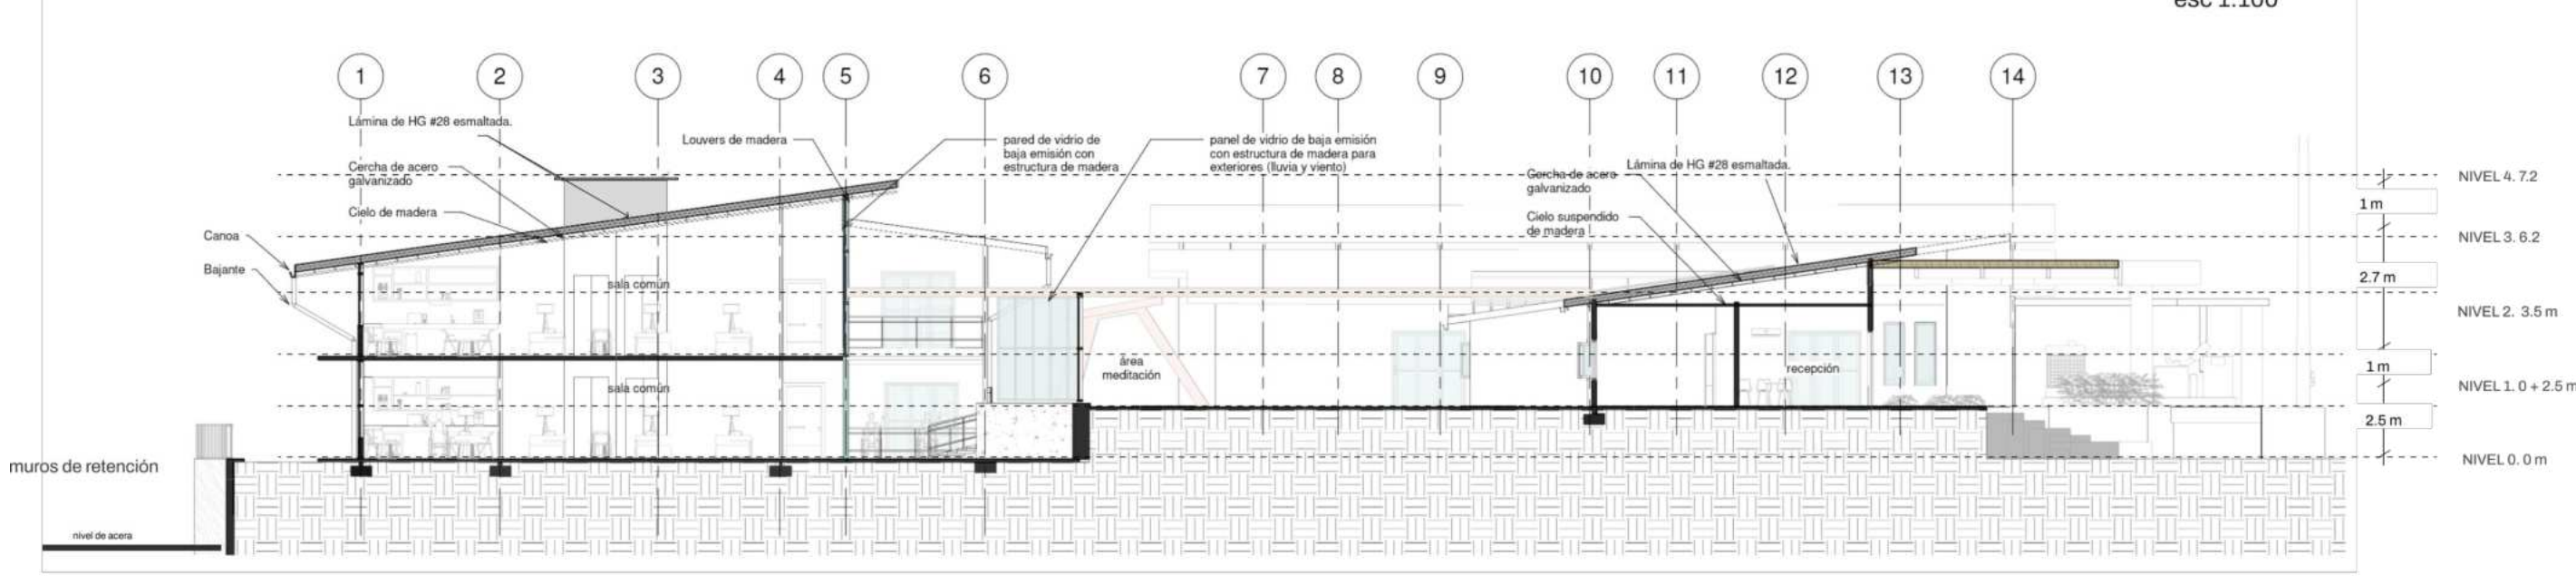

SECCIÓN D-D  
esc 1:100



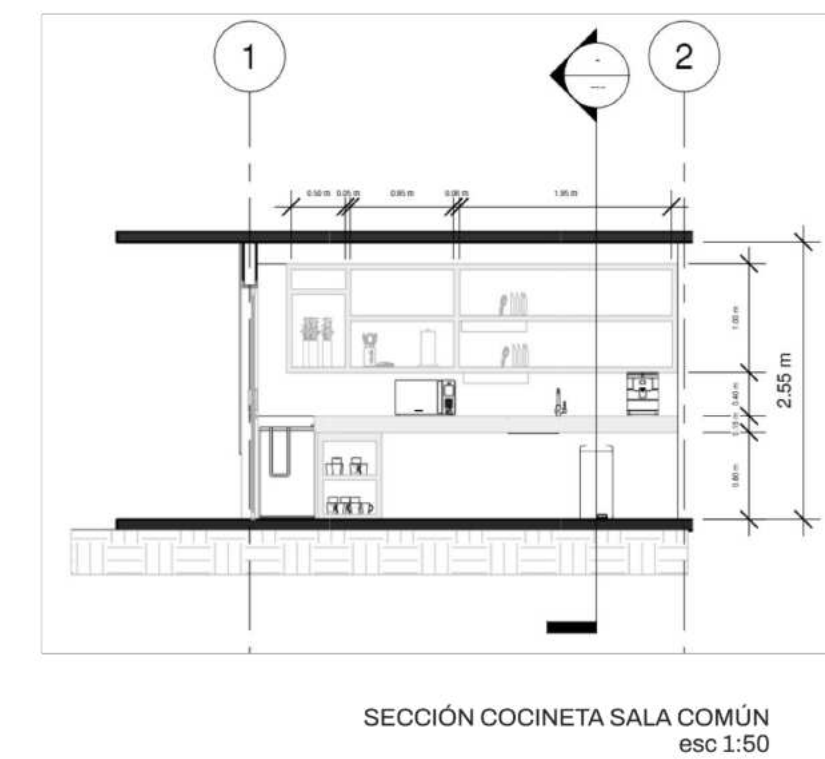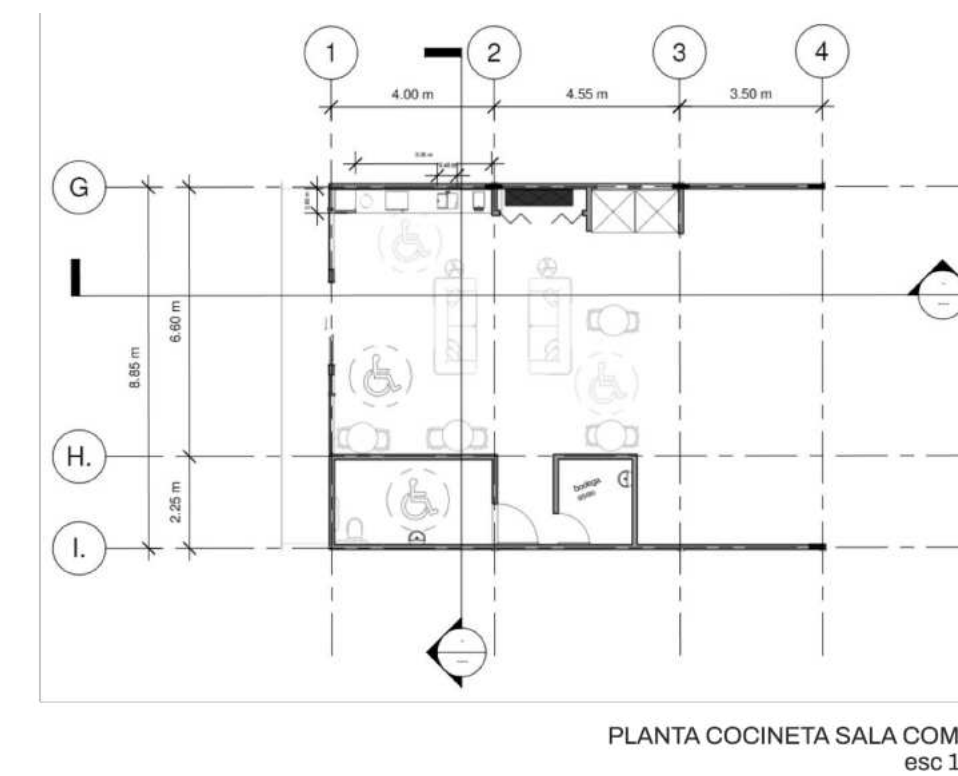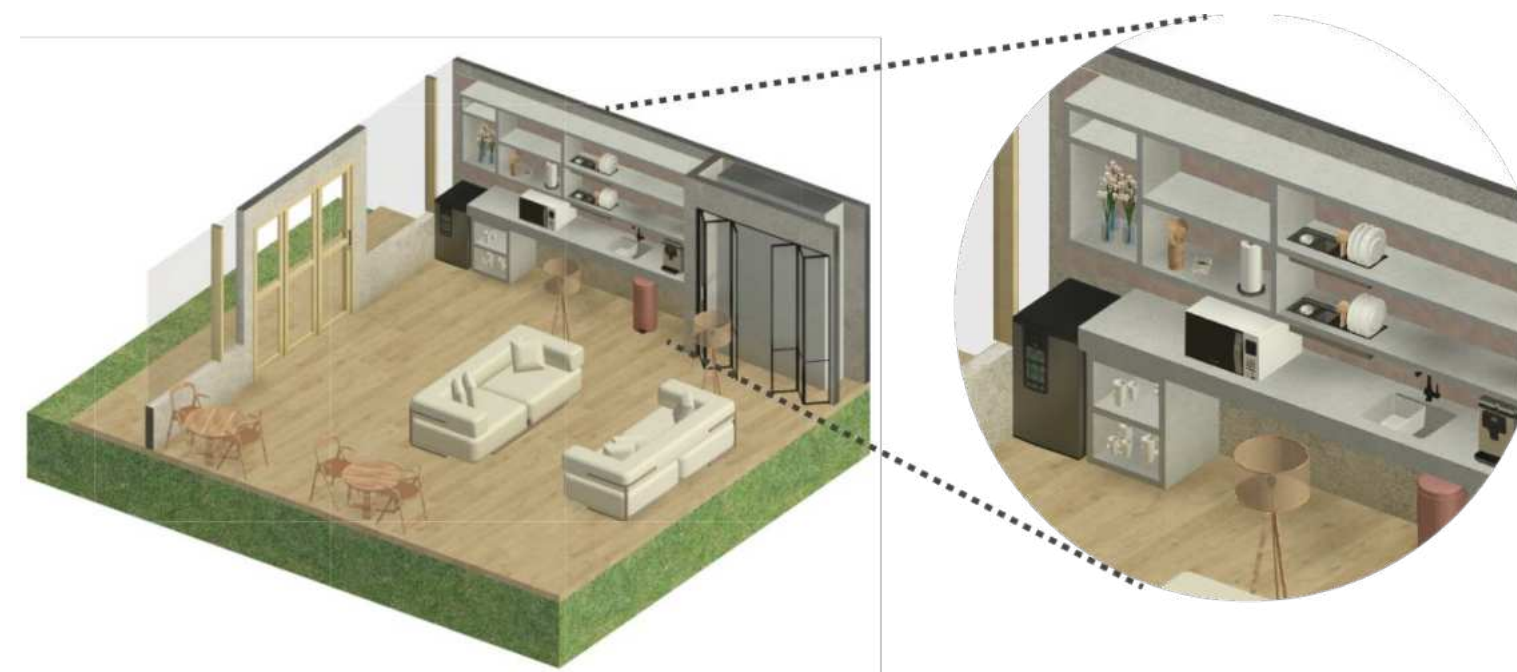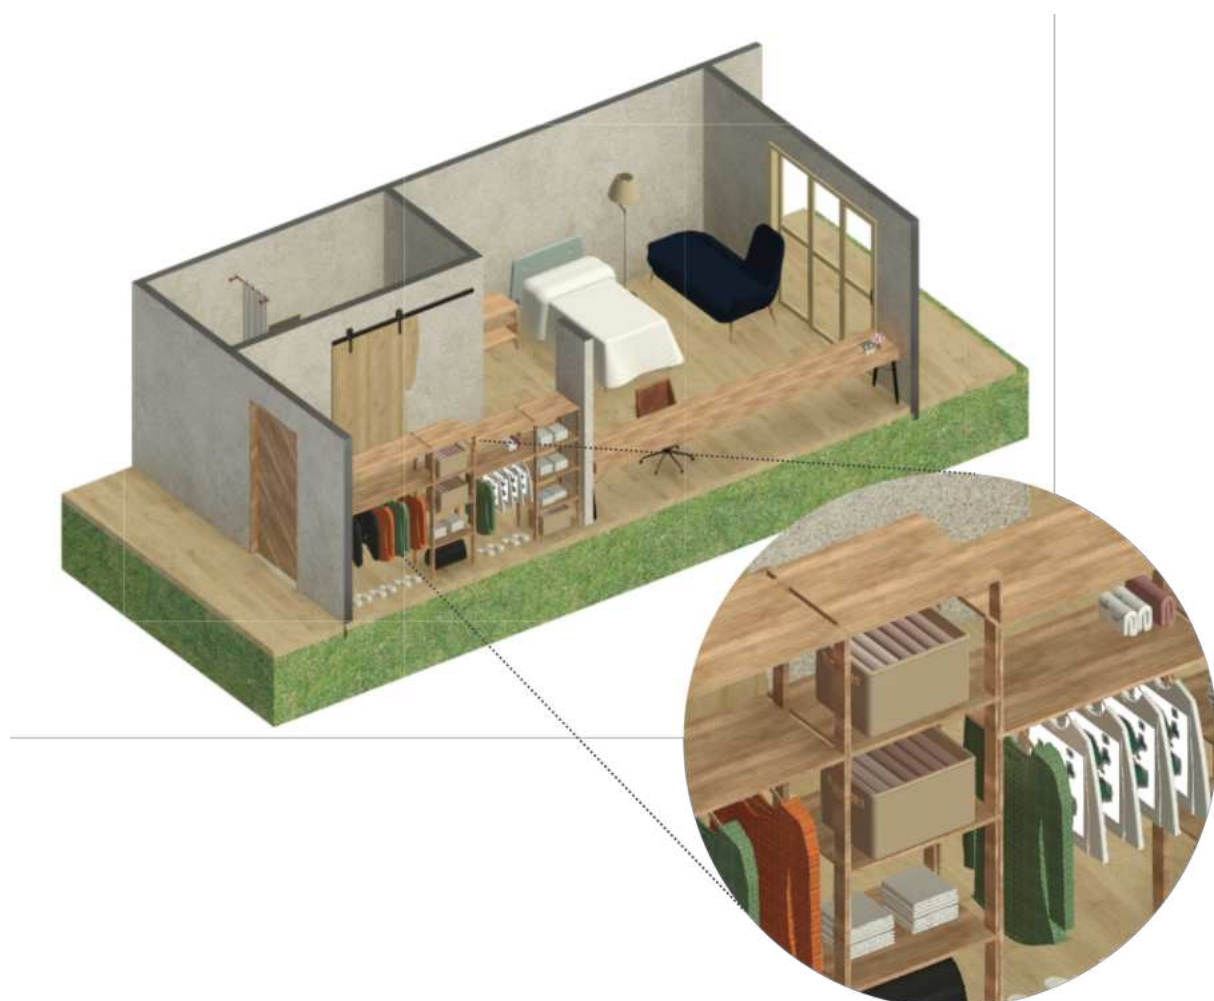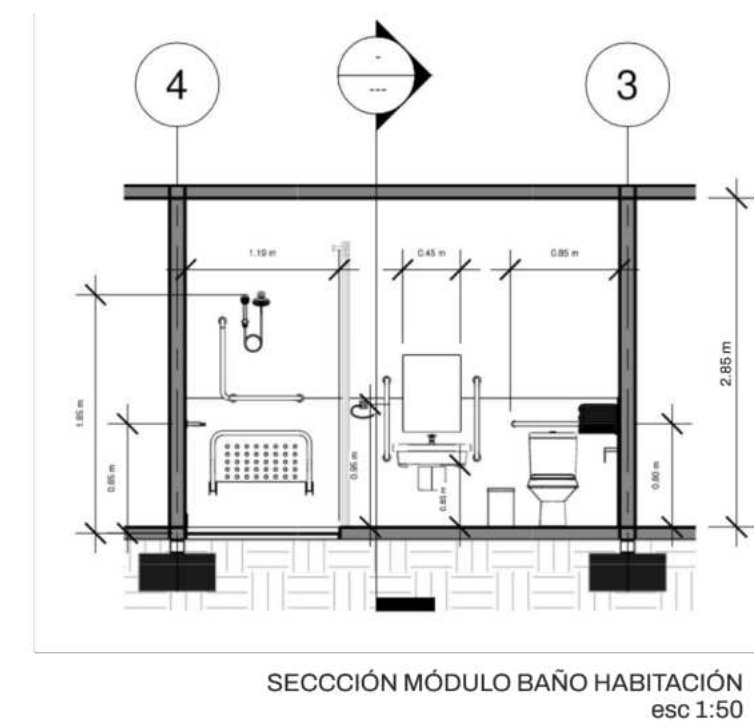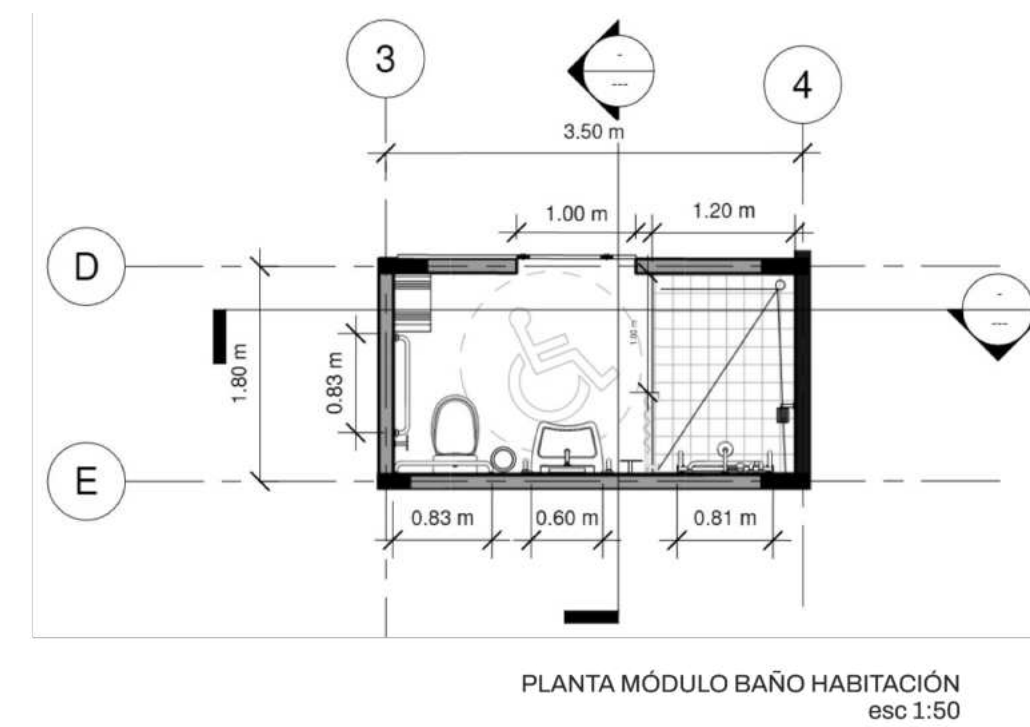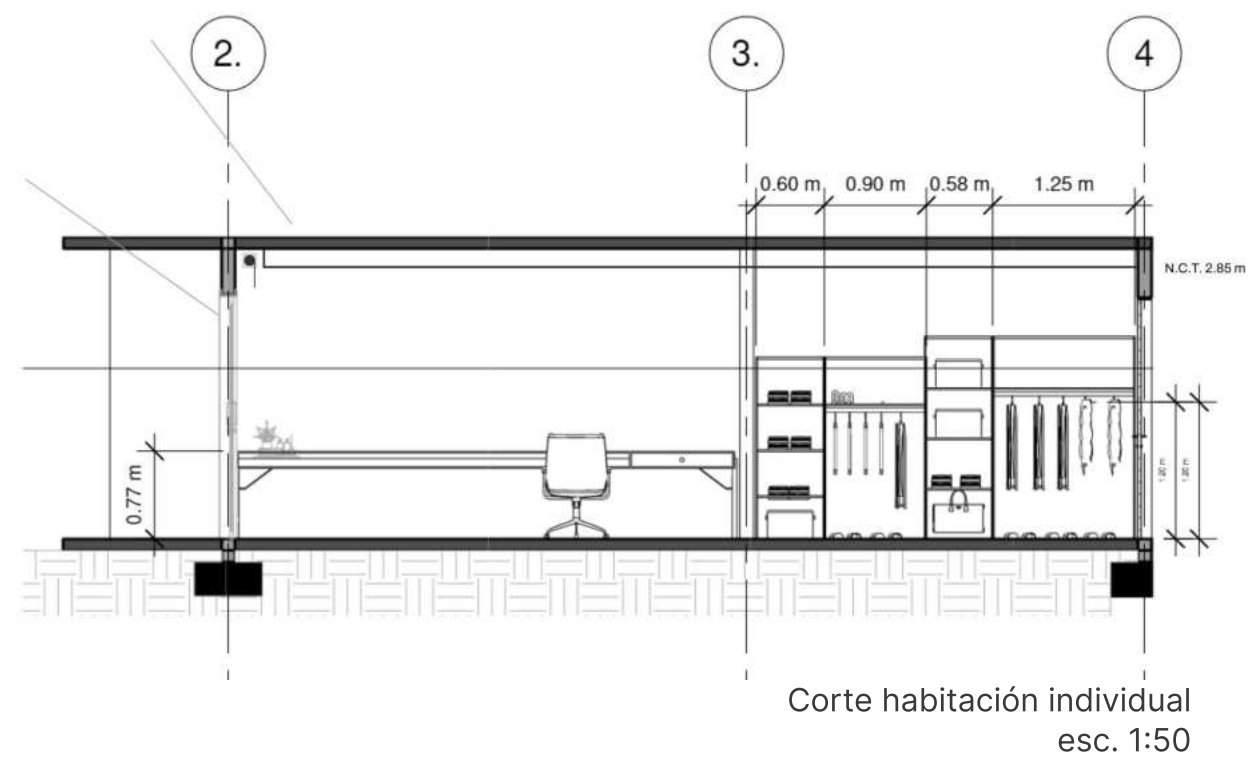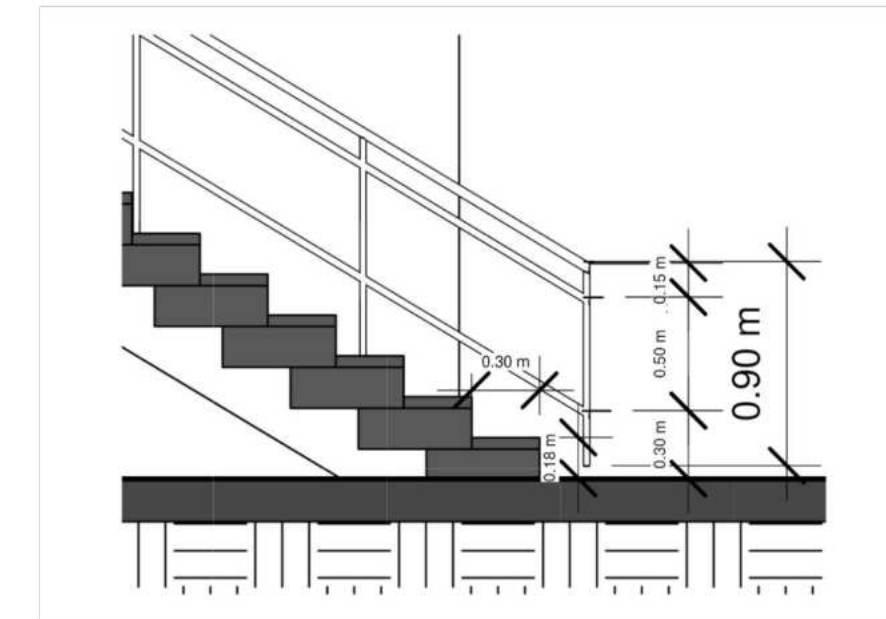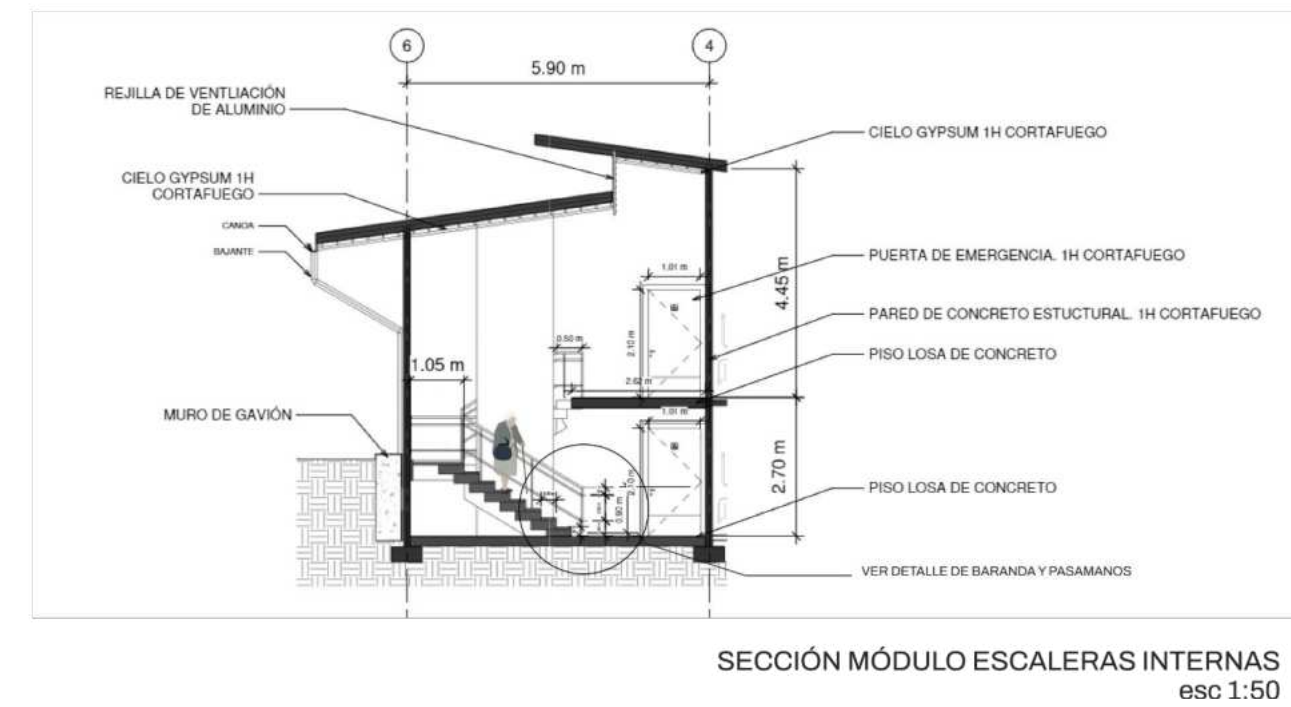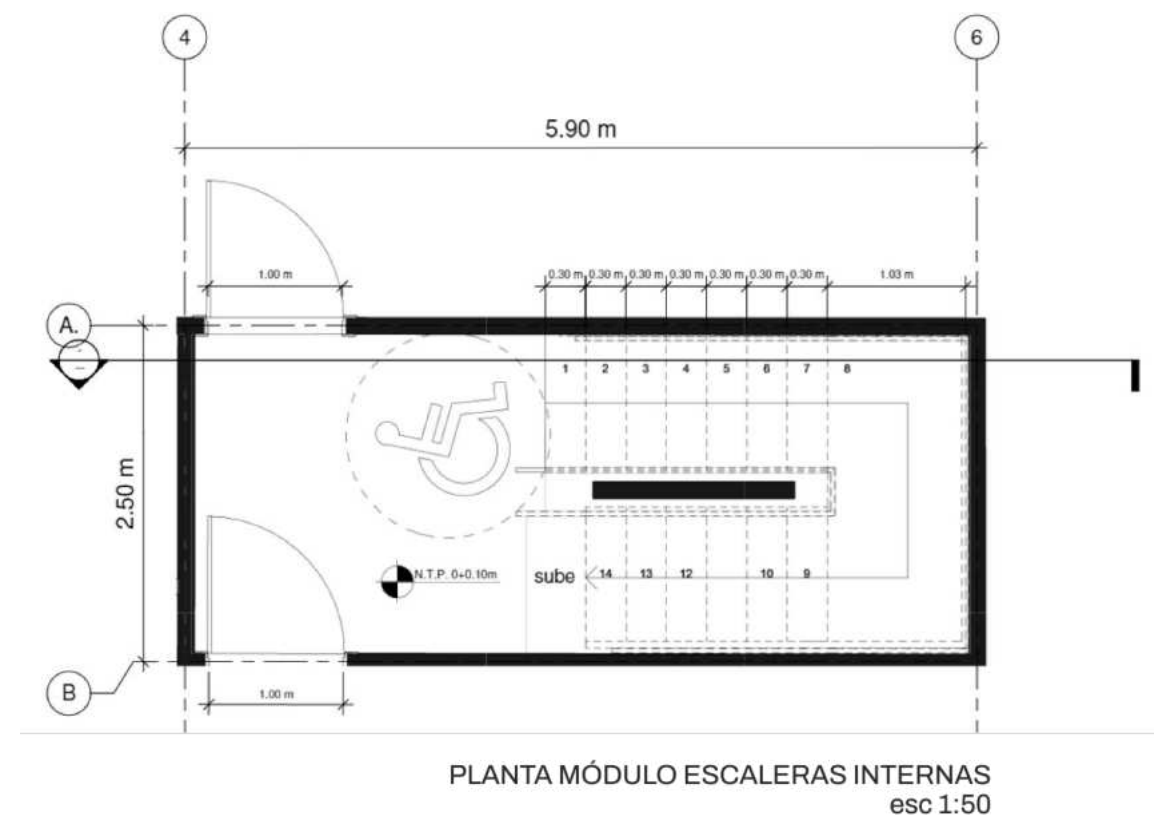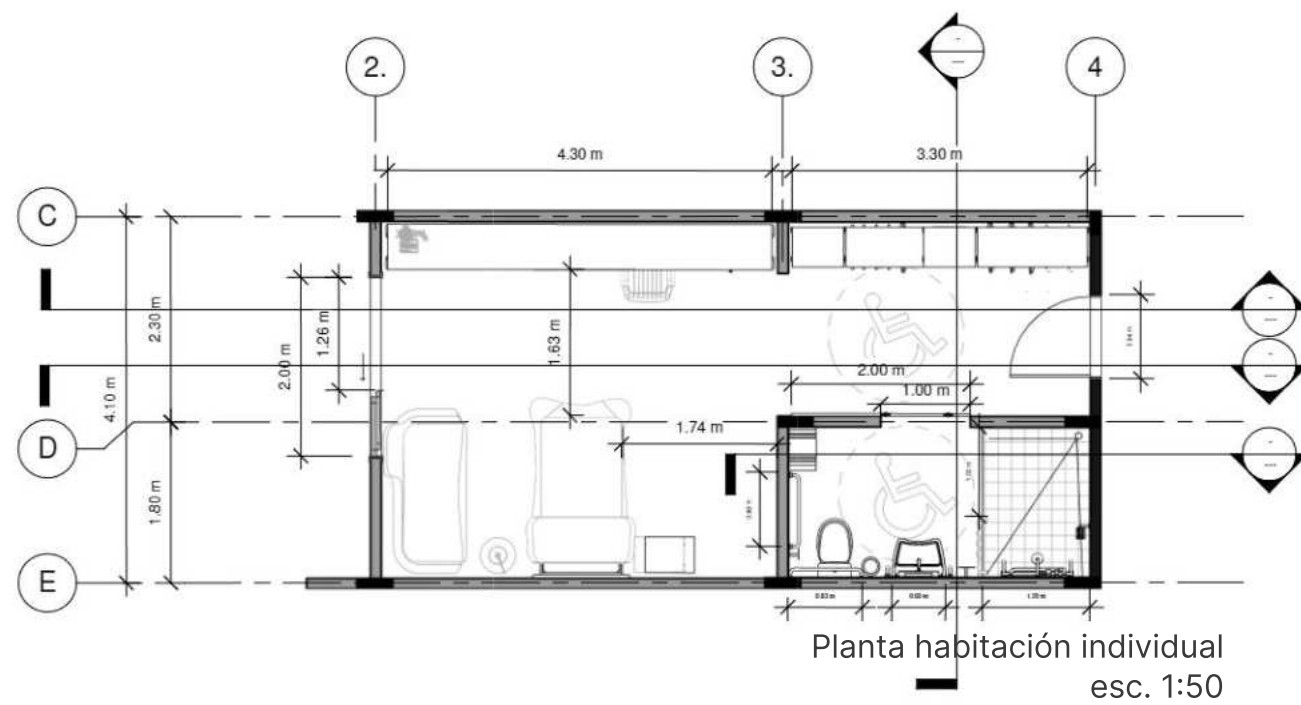





# 05

## RENDERS

CASA TALLER 4  
Taller 4

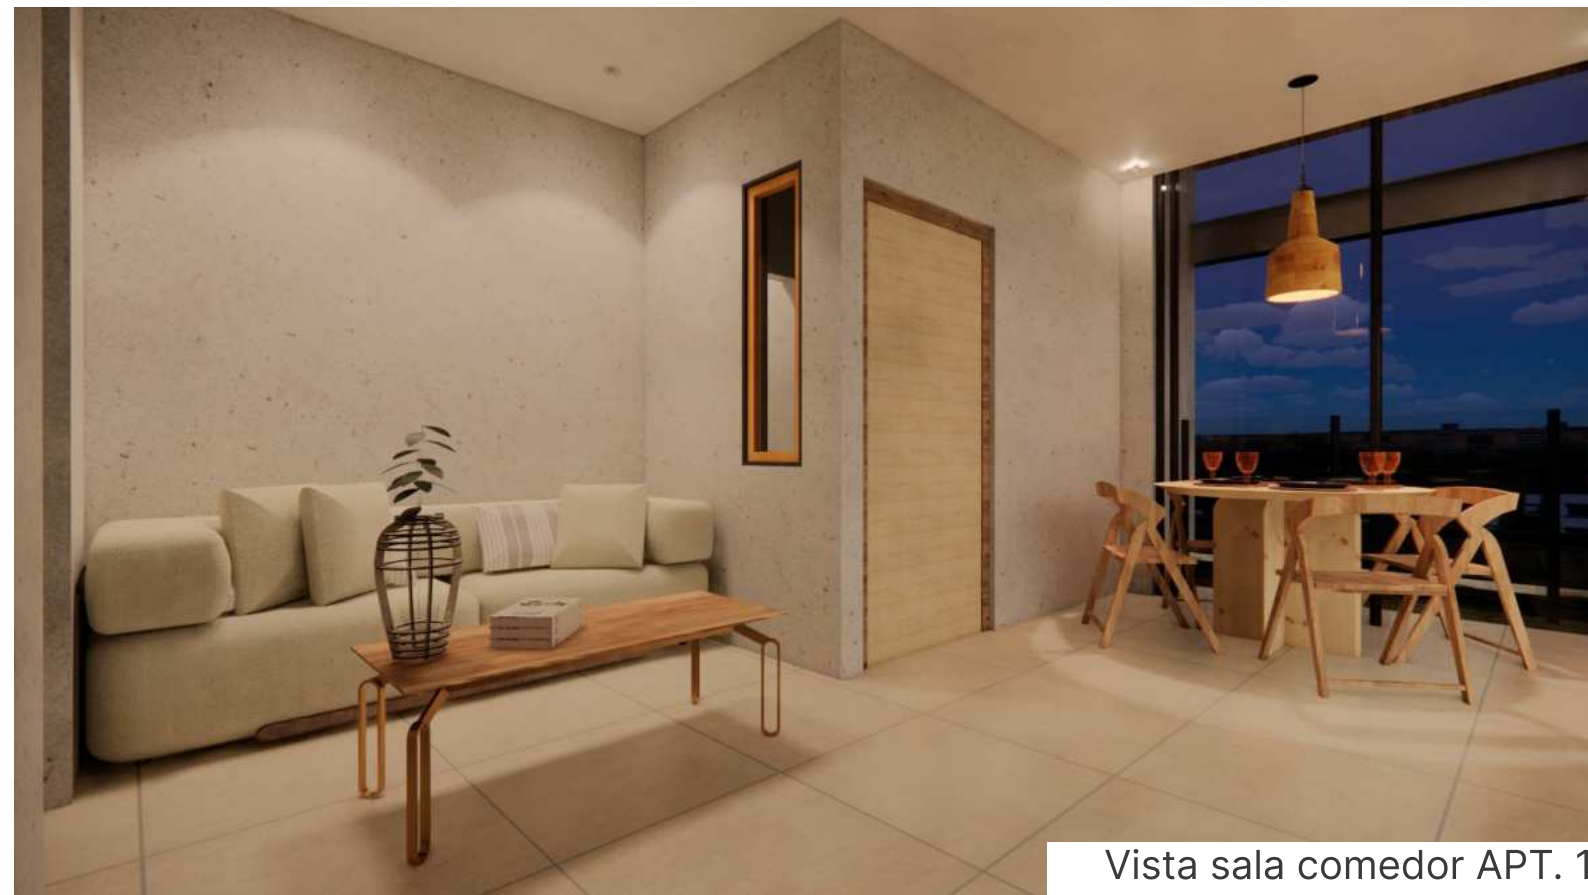

Vista sala comedor APT. 1

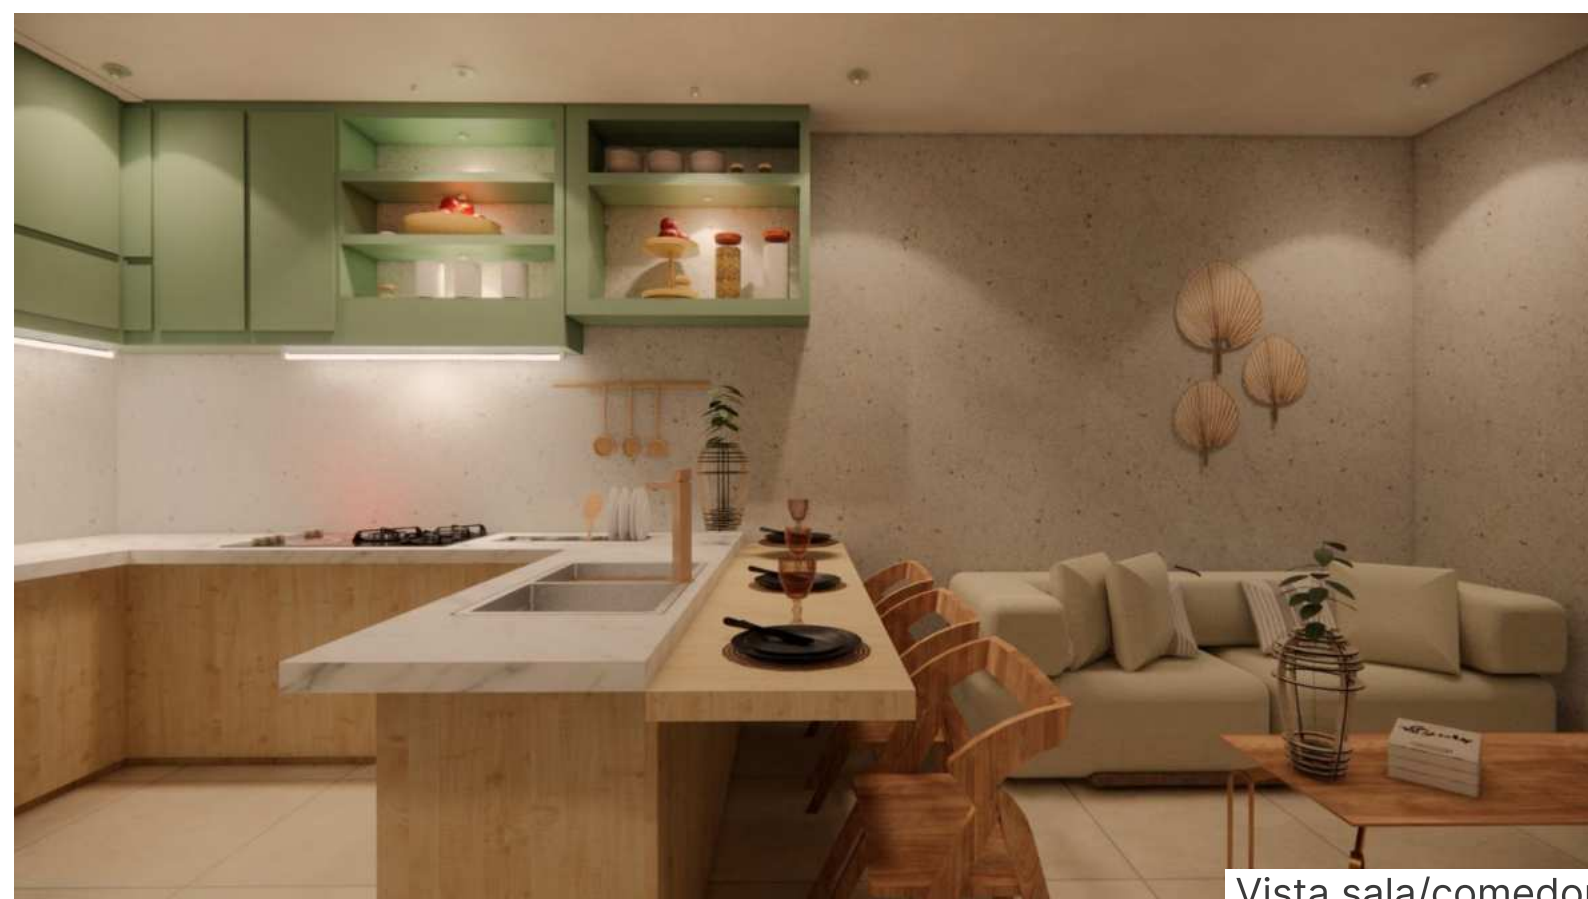

Vista sala/comedor  
APT. 2







# 05

## RENDERS

CASA TALLER 4  
Taller 4

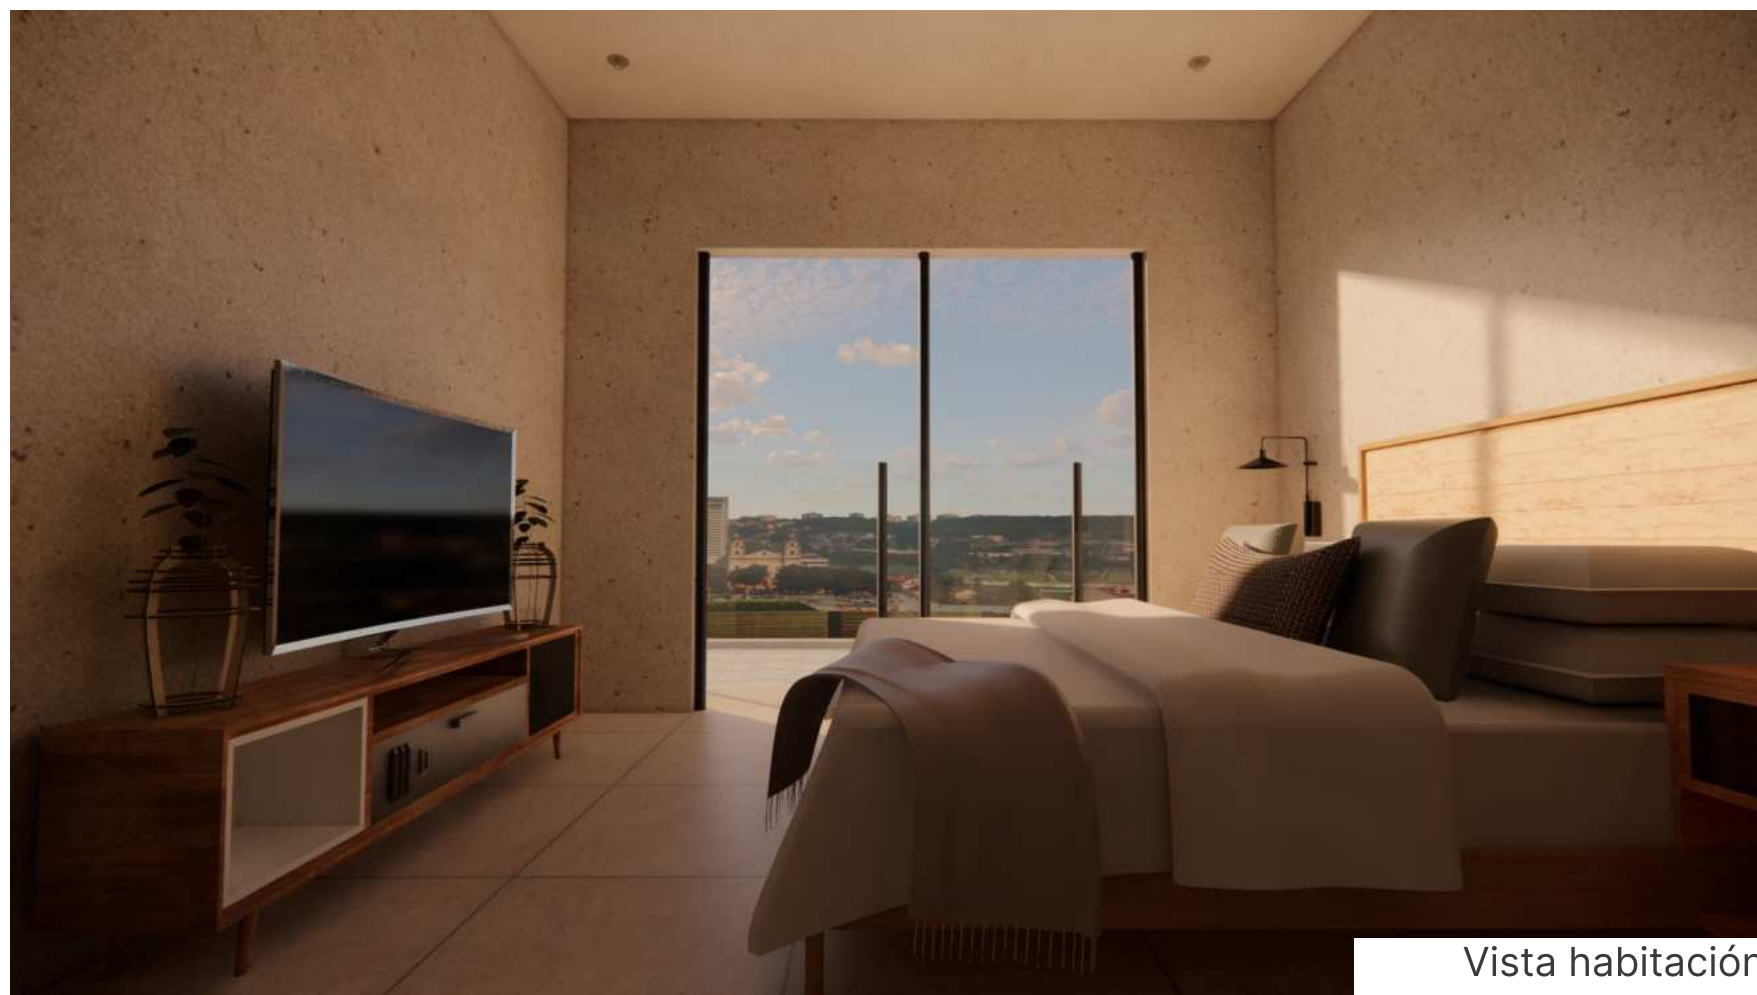


Vista habitación

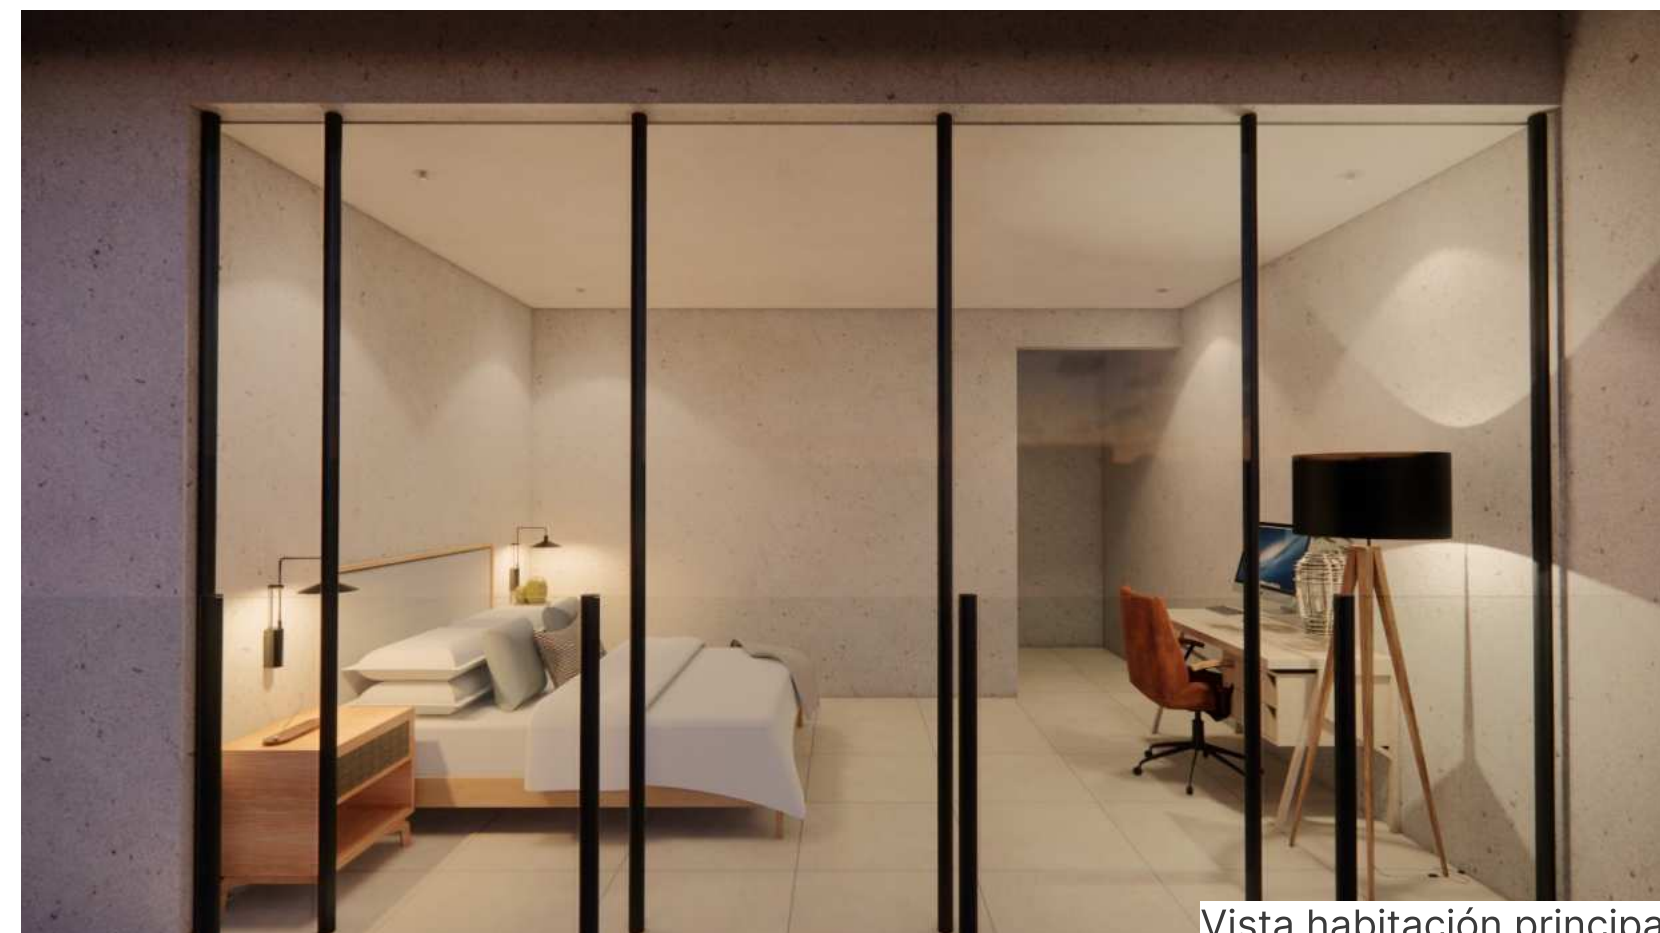

Vista habitación principal



Vista cocina comedor APT.1

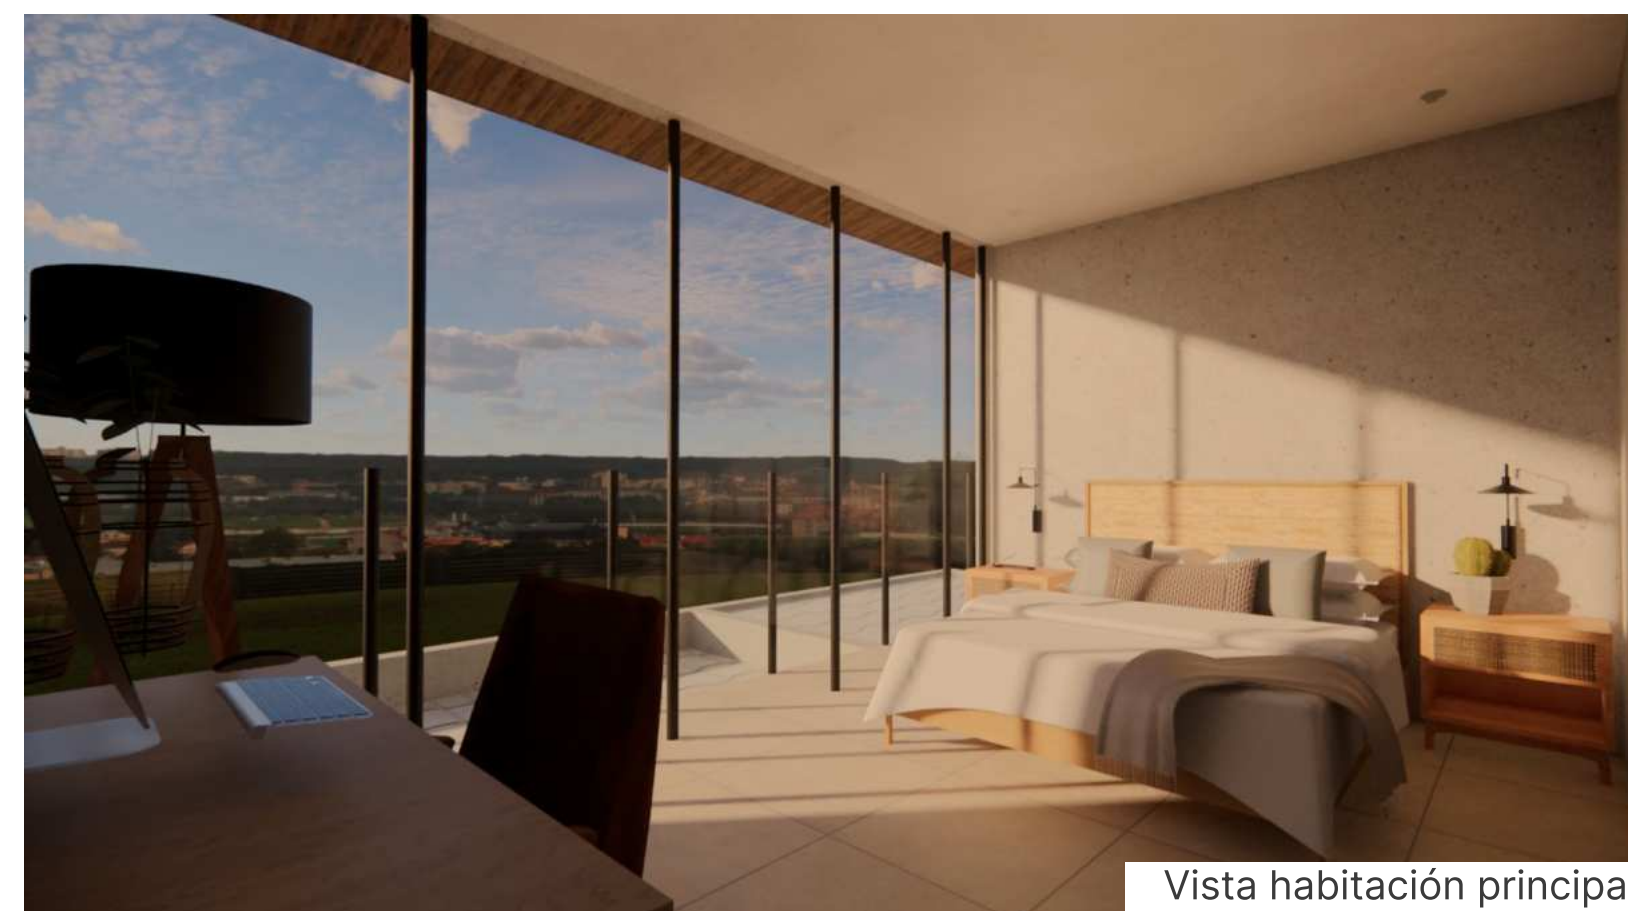

Vista habitación principal



# CONTACT

---

**phone number**    +(506) 85684666

**email**                karolina.a@hotmail.es